

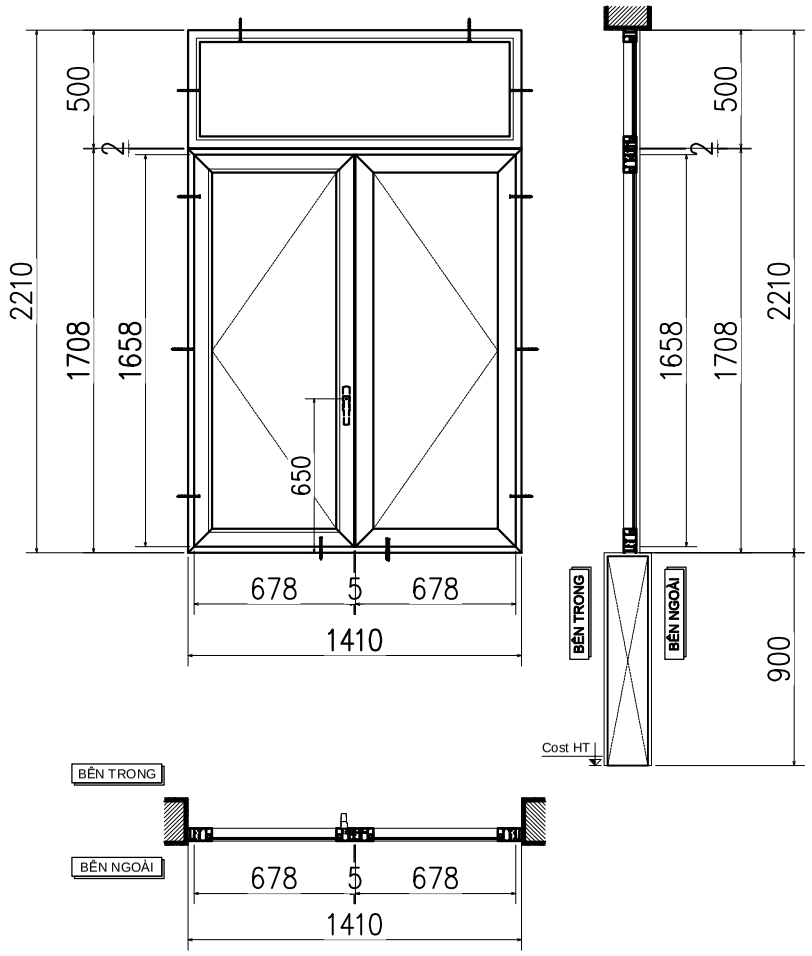


SẬP KÍNH HỘP– C3236

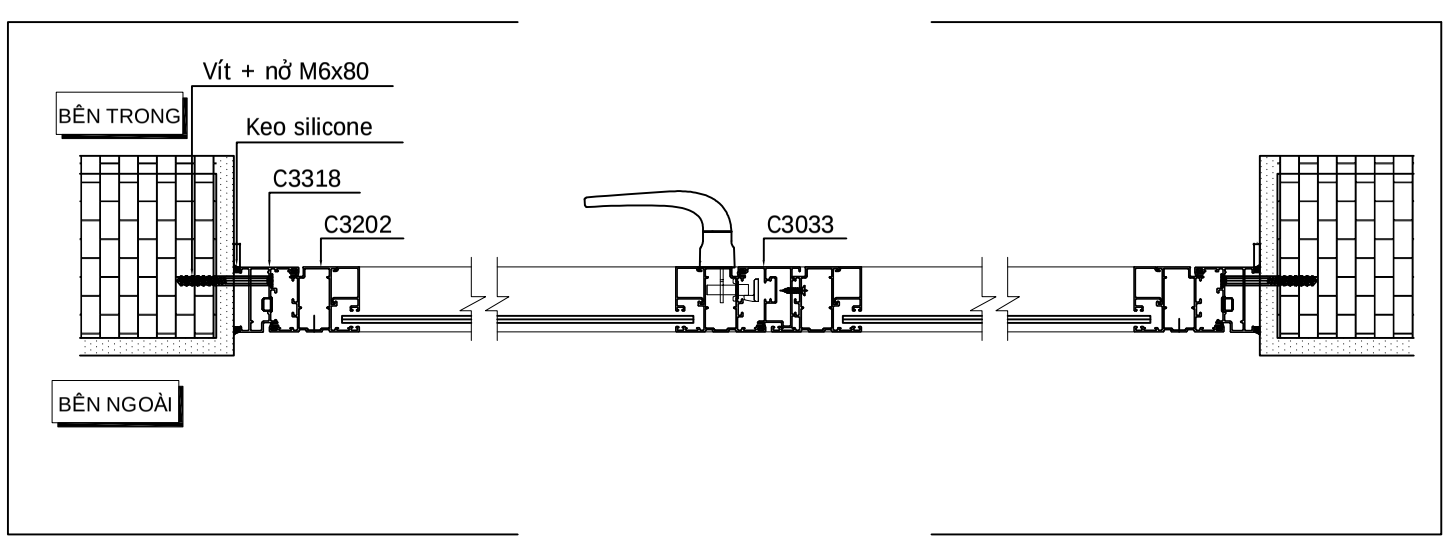

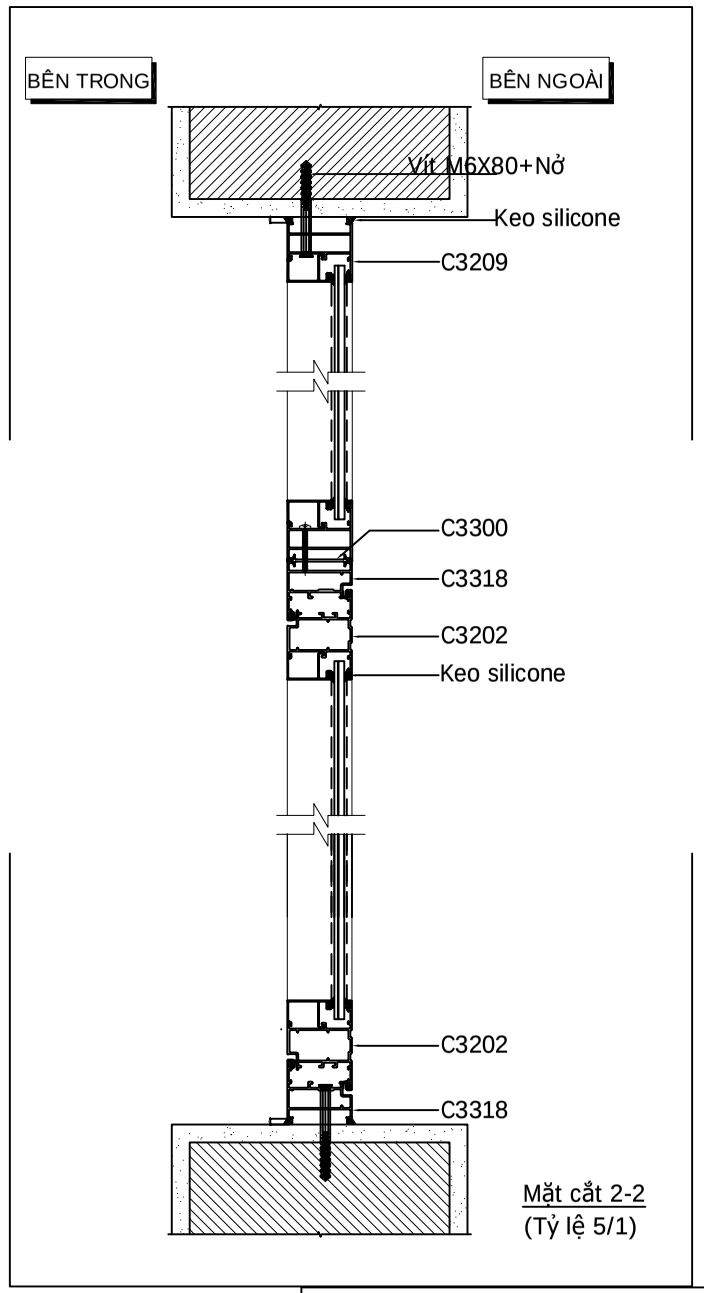

Mặt cắt 2-2
(Tỷ lệ 5/1)

BẢNG THỐNG KÊ PHỤ KIỆN CS2 CÁNH

Phụ kiện	Mã phụ kiện	Số lượng	Ghi chú
Bản A-mở quay	14"	4 cái	
Tay khoá		1 cái	Màu bạc
Thanh CĐ		1 cái	
Vấu khóa		2 cái	
Chốt âm dài		1 cái	
Chốt âm ngắn		1 cái	
Hố chốt		1 cái	
đệm chống xệ		2 bộ	
Nhựa bịt đố		1 bộ	

S1T1-1 SL: 01	QUY CÁCH	CỬA SỔ MỞ QUAY 2 CÁNH
	HỆ NHÔM	XINGFA 55
	KÍNH	HỘP 19,TRONG
	SƠN	TĨNH ĐIỆN THEO MÀU PHÊ DUYỆT
VỊ TRÍ LẮP ĐẶT	PHỤ KIỆN	DAISHIN
	GHI CHÚ	HƯỚNG NHÌN TỪ BÊN NGOÀI

CHỦ ĐẦU TƯ - INVESTOR:

XÁC NHẬN CỦA TVGS & TVTK:

DỰ ÁN - PROJECT:

GÓI THẦU:

CUNG CẤP SẢN XUẤT VÀ THI CÔNG LẮP ĐẶT PHẦN CỬA ĐI, CỬA SỔ, VÁCH NHÔM KÍNH

NHÀ THẦU:

CÔNG TY CỔ NHÔM AN PHÚ

Địa chỉ: Thôn Khê Nữ - X. Phúc Thịnh - TP. Hà Nội

Chủ trì: Project manager:	
Kiểm tra: check by:	
Thiết kế: design by:	Ks. Đặng Anh Dũng


TÊN BẢN VẼ - NAME DRAWING:

Sửa đổi


Lần/rev	Ngày/date	Xác nhận/confirm


Bản vẽ số/ drawing:

Ngày tháng/date:

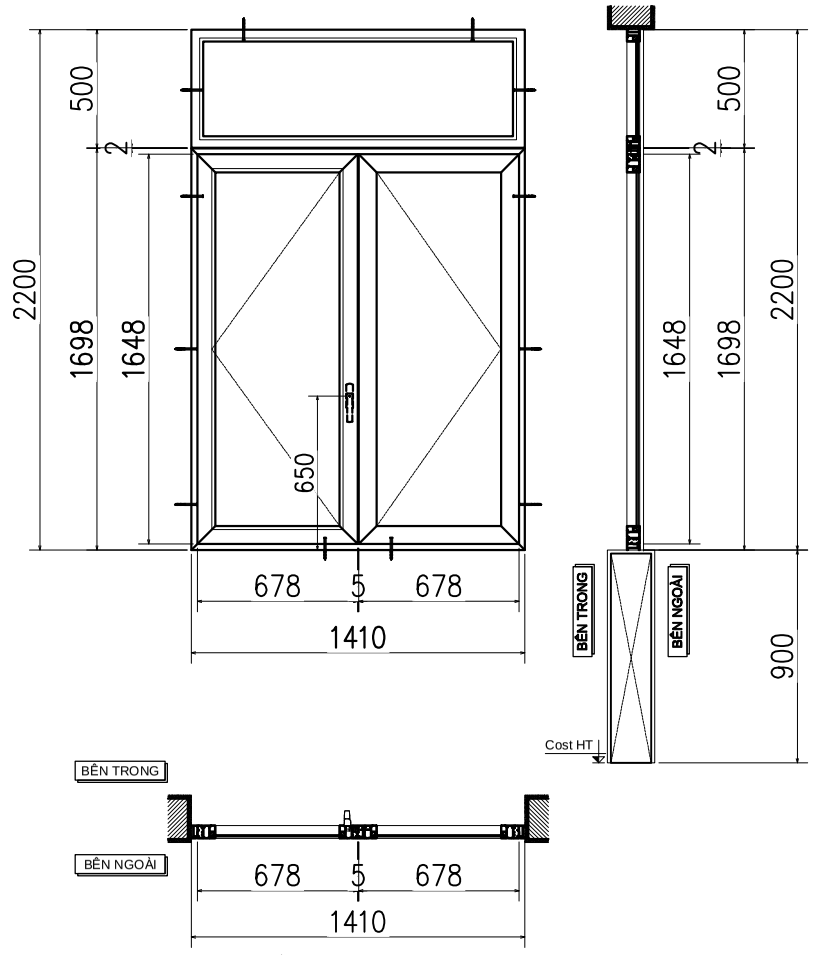

SẬP KÍNH HỘP– C3236

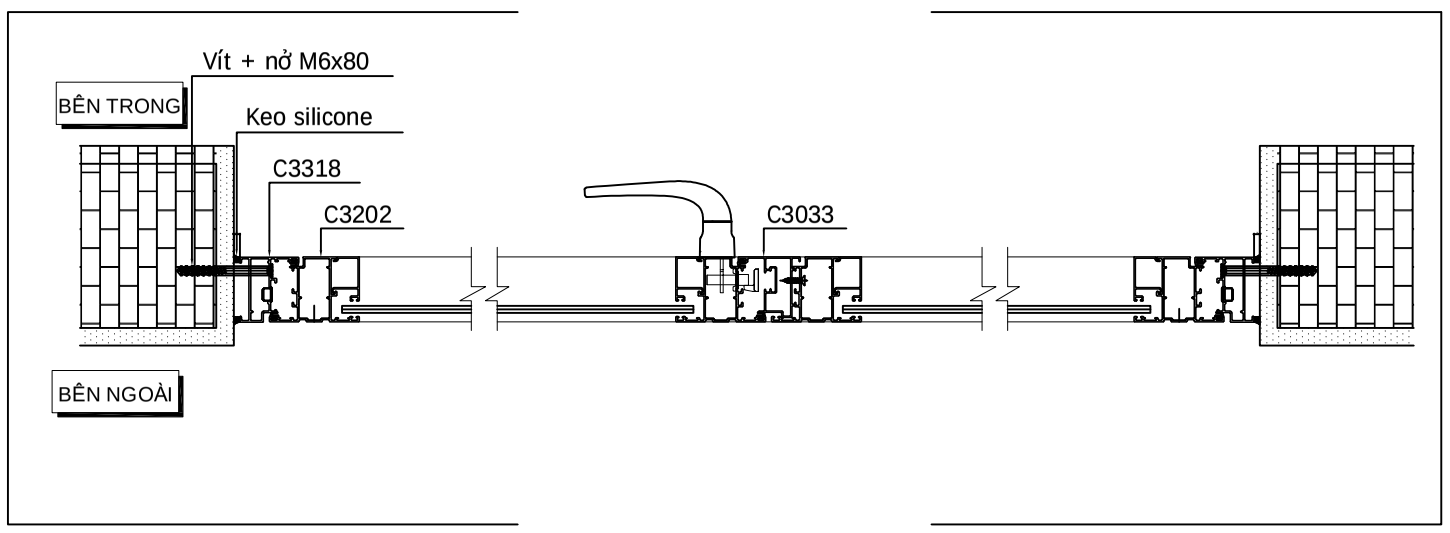

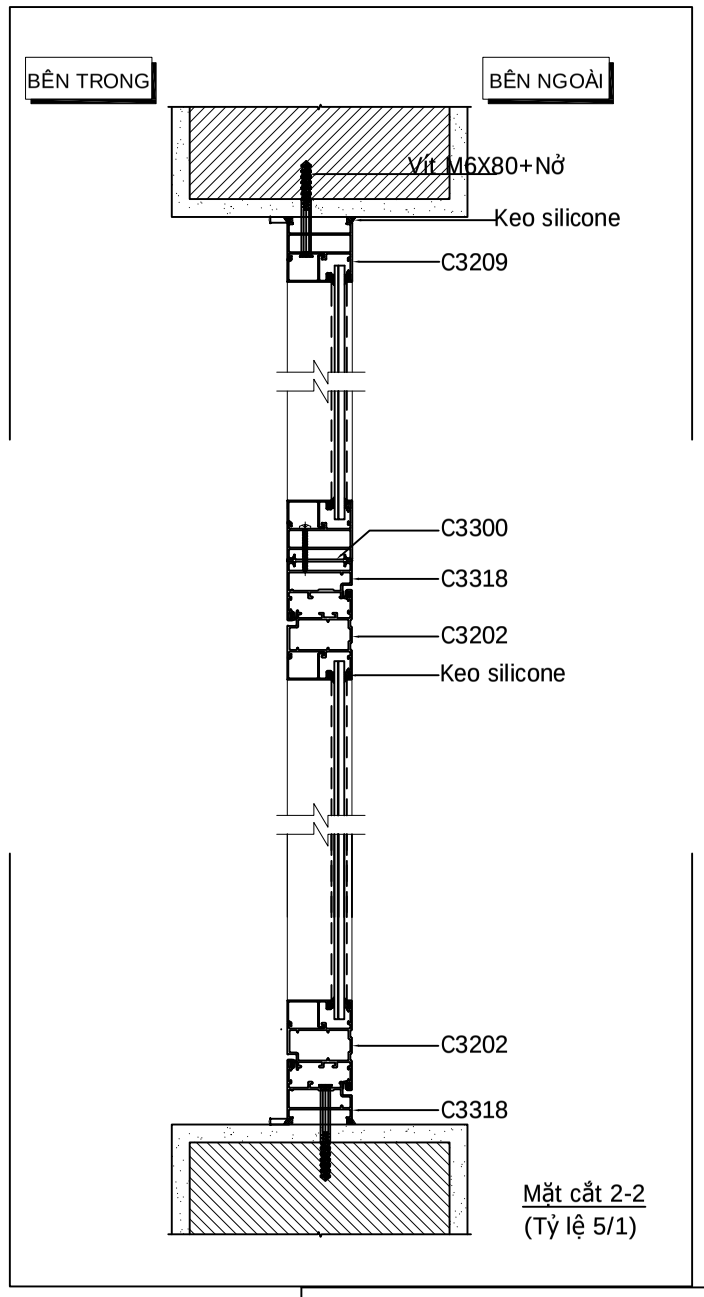

Mặt cắt 2-2
(Tỷ lệ 5/1)

BẢNG THỐNG KÊ PHỤ KIỆN CS2 CÁNH

Phụ kiện	Mã phụ kiện	Số lượng	Ghi chú
Bản A-mở quay	14"	4 cái	
Tay khoá		1 cái	Màu bạc
Thanh CĐ		1 cái	
Vấu khóa		2 cái	
Chốt âm dài		1 cái	
Chốt âm ngắn		1 cái	
Hố chốt		1 cái	
đệm chống xệ		2 bộ	
Nhựa bịt đố		1 bộ	

S1T1-2 SL: 01	QUY CÁCH	CỬA SỔ MỞ QUAY 2 CÁNH
	HỆ NHÔM	XINGFA 55
	KÍNH	HỘP 19,TRONG
	SƠN	TĨNH ĐIỆN THEO MÀU PHÊ DUYỆT
VỊ TRÍ LẮP ĐẶT	PHỤ KIỆN	DAISHIN
	GHI CHÚ	HƯỚNG NHÌN TỪ BÊN NGOÀI

CHỦ ĐẦU TƯ - INVESTOR:

XÁC NHẬN CỦA TVGS & TVTK:

DỰ ÁN - PROJECT:

GÓI THẦU:

CUNG CẤP SẢN XUẤT VÀ THI CÔNG LẮP ĐẶT PHẦN CỬA ĐI, CỬA SỔ, VÁCH NHÔM KÍNH

NHÀ THẦU:

CÔNG TY CỔ NHÔM AN PHÚ

Địa chỉ: Thôn Khê Nữ - X. Phúc Thịnh - TP. Hà Nội

Chủ trì: Project manager:	
Kiểm tra: check by:	
Thiết kế: design by:	Ks. Đặng Anh Dũng


TÊN BẢN VẼ - NAME DRAWING:

Sửa đổi


Lần/rev	Ngày/date	Xác nhận/confirm

Bản vẽ số/ drawing:


Ngày tháng/date:

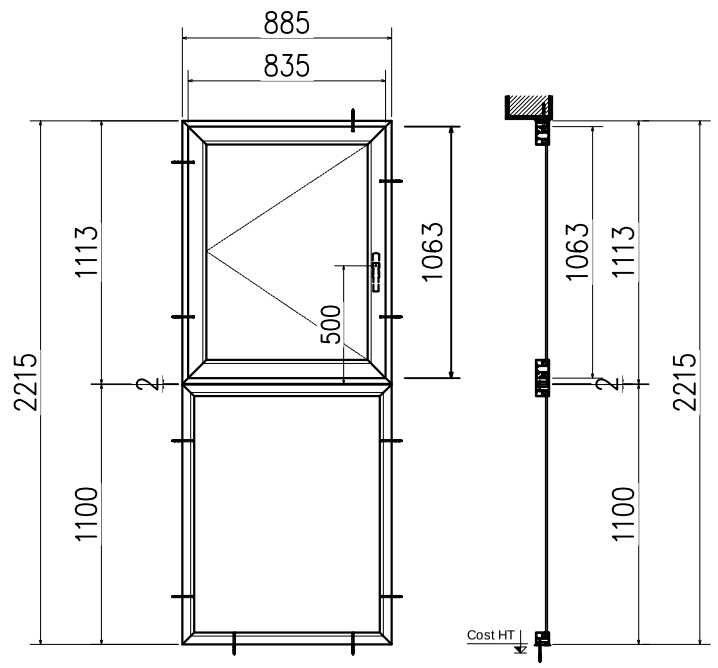


C3236

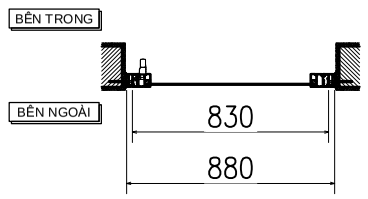

SẬP KÍNH HỘP– C3236

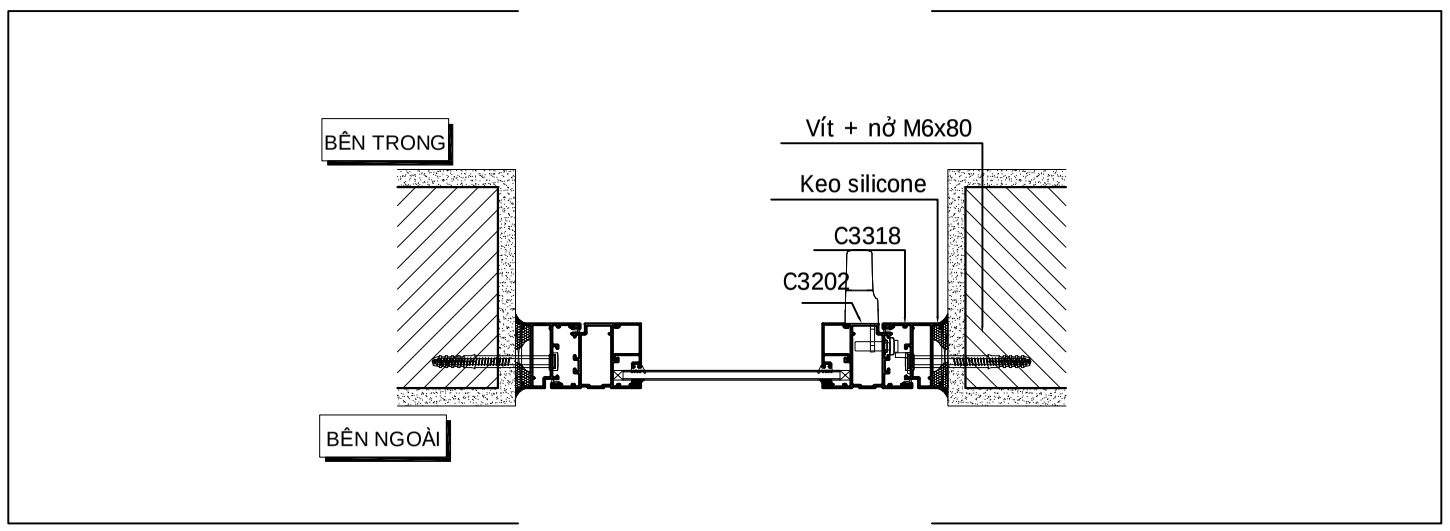

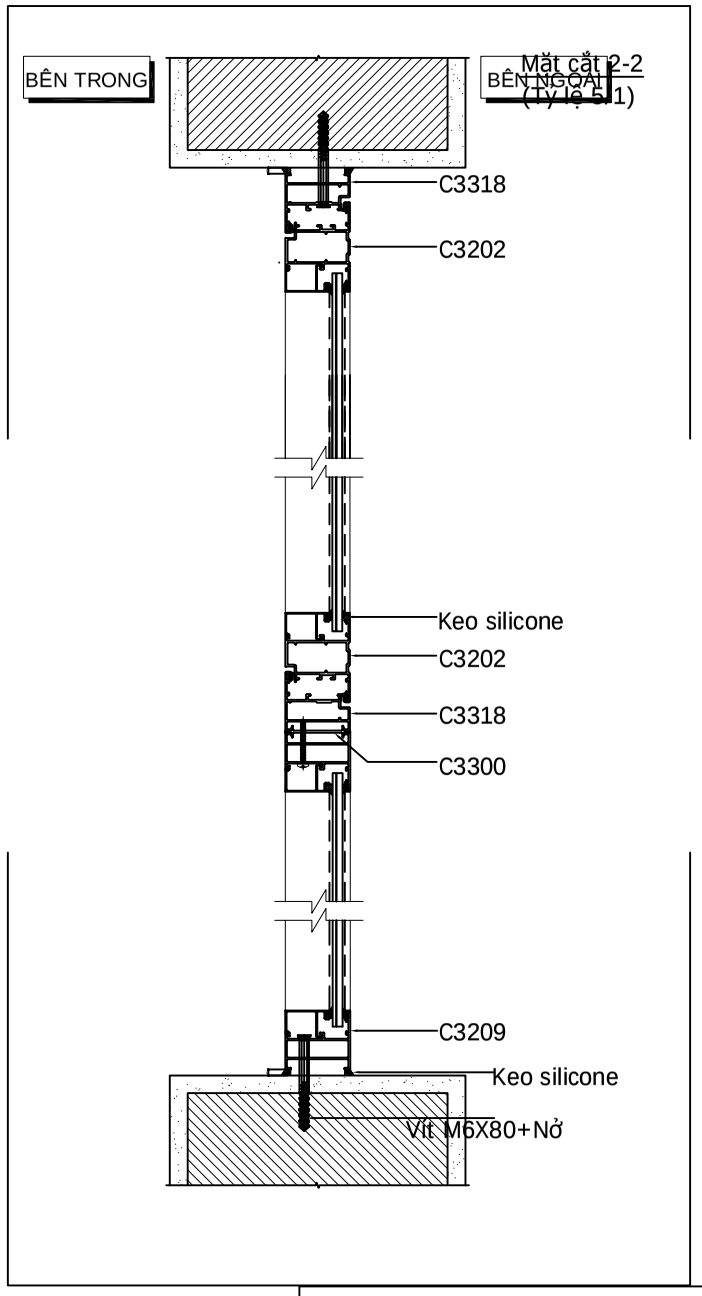

BẢNG THỐNG KÊ PHỤ KIỆN CS2 CÁNH			
Phụ kiện	Mã phụ kiện	Số lượng	Ghi chú
Bản A	16"	2 cái	
Tay khoá		1 cái	Màu bạc
Thanh CĐ		1 cái	
Vấu khóa		2 cái	
		1 cái	
		1 cái	
đệm chống xệ		1 bộ	

S2T1 SL: 01	QUY CÁCH	CỬA SỔ MỞ QUAY 1 CÁNH
	HỆ NHÔM	XINGFA 55
	KÍNH	HỘP 19,TRONG
	SƠN	TĨNH ĐIỆN THEO MÀU PHÊ DUYỆT
VỊ TRÍ LẮP ĐẶT	PHỤ KIỆN	DAISHIN
	GHI CHÚ	HƯỚNG NHÌN TỪ BÊN NGOÀI

CHỦ ĐẦU TƯ - INVESTOR:

XÁC NHẬN CỦA TVGS & TVTK:

DỰ ÁN - PROJECT:

GÓI THẦU:

CUNG CẤP SẢN XUẤT VÀ THI CÔNG LẮP ĐẶT PHẦN CỬA ĐI, CỬA SỔ, VÁCH NHÔM KÍNH

NHÀ THẦU:

CÔNG TY CỔ NHÔM AN PHÚ

Địa chỉ: Thôn Khê Nữ - X. Phúc Thịnh - TP. Hà Nội

Chủ trì: Project manager:	
Kiểm tra: check by:	
Thiết kế: design by:	Ks. Đặng Anh Dũng

TÊN BẢN VẼ - NAME DRAWING:


Sửa đổi


Lần/rev	Ngày/date	Xác nhận/confirm

Bản vẽ số/ drawing:


Ngày tháng/date:

GHI CHÚ:
-KÍCH THƯỚC SẢN XUẤT LÀ KÍCH THƯỚC ĐỂ GIA CÔNG CỬA THÀNH PHẨM
-CHIỀU MỞ CỬA TỪNG VỊ TRÍ XEM TRÊN BẢN VẼ MẶT BẰNG
-KHOAN LỖ THOÁT NƯỚC MƯA VÀ LỖ LẮP ĐẶT TRƯỚC KHI RA CÔNG TRƯỜNG

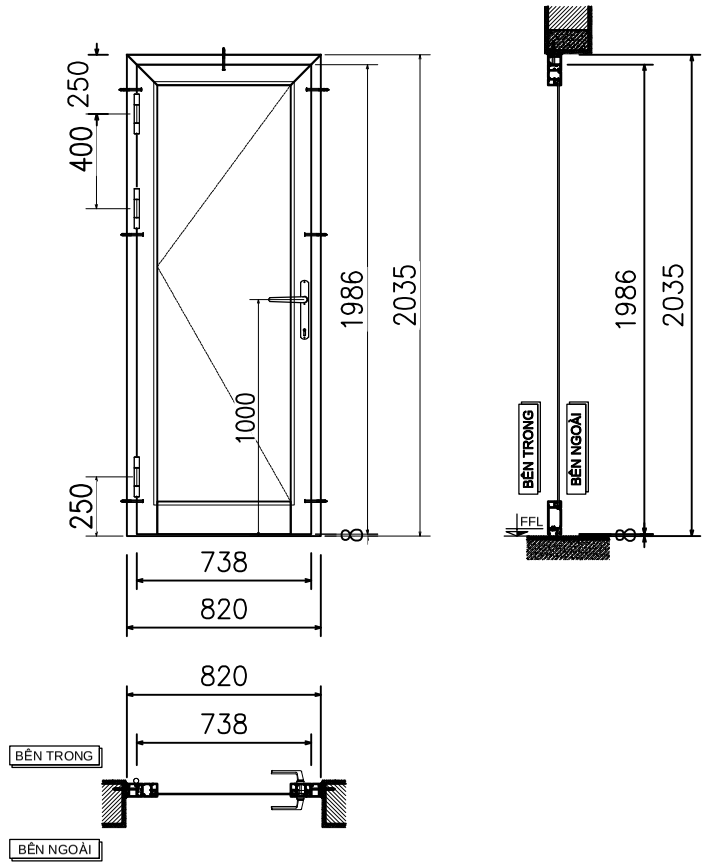

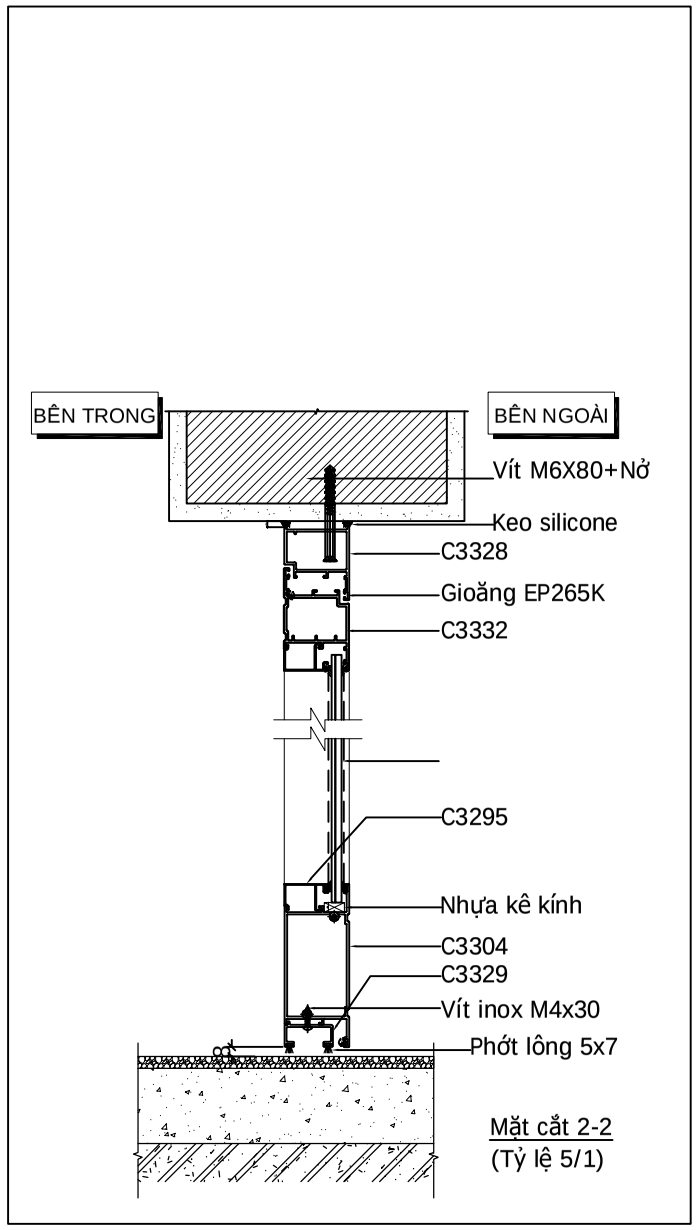

Mặt cắt 2-2
(Tỷ lệ 5/1)

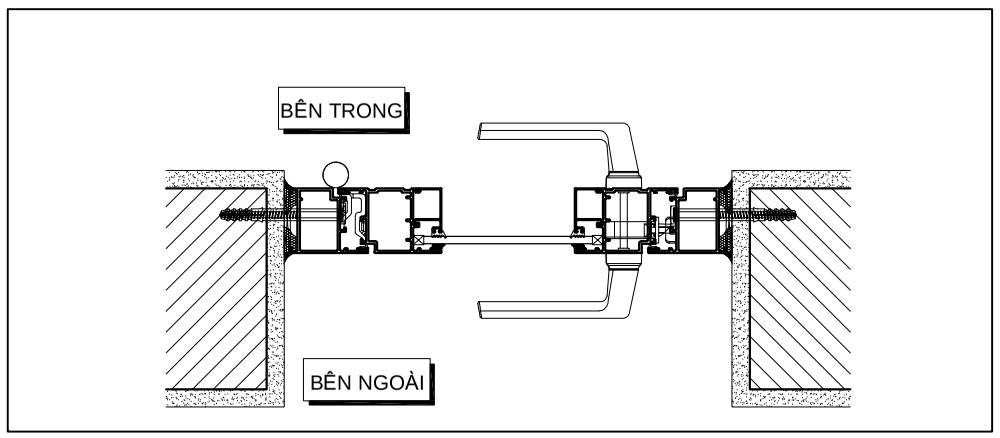

BẢNG THỐNG KÊ PHỤ KIỆN- KHÓA ĐA ĐIỂM			
Phụ kiện	Mã phụ kiện	Số lượng	Ghi chú
Bản lề bi đũa		3cái	Màu bạc
Tay khoá		1 cái	Màu bạc
Thân khoá		1 cái	Đơn ĐIỂM
Lõi khoá		1 cái	MỞ trong
		1 cái	

WCT1 SL: 01 BỘ	QUY CÁCH	CỬA SỔ MỞ QUAY 1 CÁNH LIỀN VÁCH KÍNH
	HỆ NHÔM	XINGFA 55
	KÍNH	8.38 SỮA
	SƠN	TĨNH ĐIỆN THEO MÀU PHÊ DUYỆT
VỊ TRÍ LẮP ĐẶT	PHỤ KIỆN	DAISHIN
	GHI CHÚ	HƯỚNG NHÌN TỪ BÊN NGOÀI

CHỦ ĐẦU TƯ - INVESTOR:

XÁC NHẬN CỦA TVGS & TVTK:

DỰ ÁN - PROJECT:

GÓI THẦU:
CUNG CẤP SẢN XUẤT VÀ THI CÔNG LẮP ĐẶT PHẦN CỬA ĐI, CỬA SỔ, VÁCH NHÔM KÍNH

NHÀ THẦU:
CÔNG TY CỔ NHÔM AN PHÚ
Địa chỉ: Thôn Khê Nữ - X. Phúc Thịnh - TP. Hà Nội

Chủ trì: Project manager:	
Kiểm tra: check by:	
Thiết kế: design by:	Ks. Đặng Anh Dũng


TÊN BẢN VẼ - NAME DRAWING:

Sửa đổi


Lần/rev	Ngày/date	Xác nhận/confirm

Bản vẽ số/ drawing:	
Ngày tháng/date:	


GHI CHÚ:
-KÍCH THƯỚC SẢN XUẤT LÀ KÍCH THƯỚC ĐỂ GIA CÔNG CỬA THÀNH PHẨM
-CHIỀU MỞ CỬA TỪNG VỊ TRÍ XEM TRÊN BẢN VẼ MẶT BẰNG
-KHOAN LỖ THOÁT NƯỚC MƯA VÀ LỖ LẮP ĐẶT TRƯỚC KHI RA CÔNG TRƯỜNG

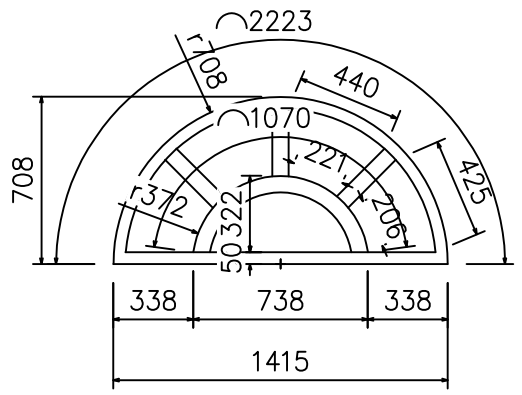


KH: D1T2-1
SL: 01
C3209+C3236=2750
C3203+C3236=1600

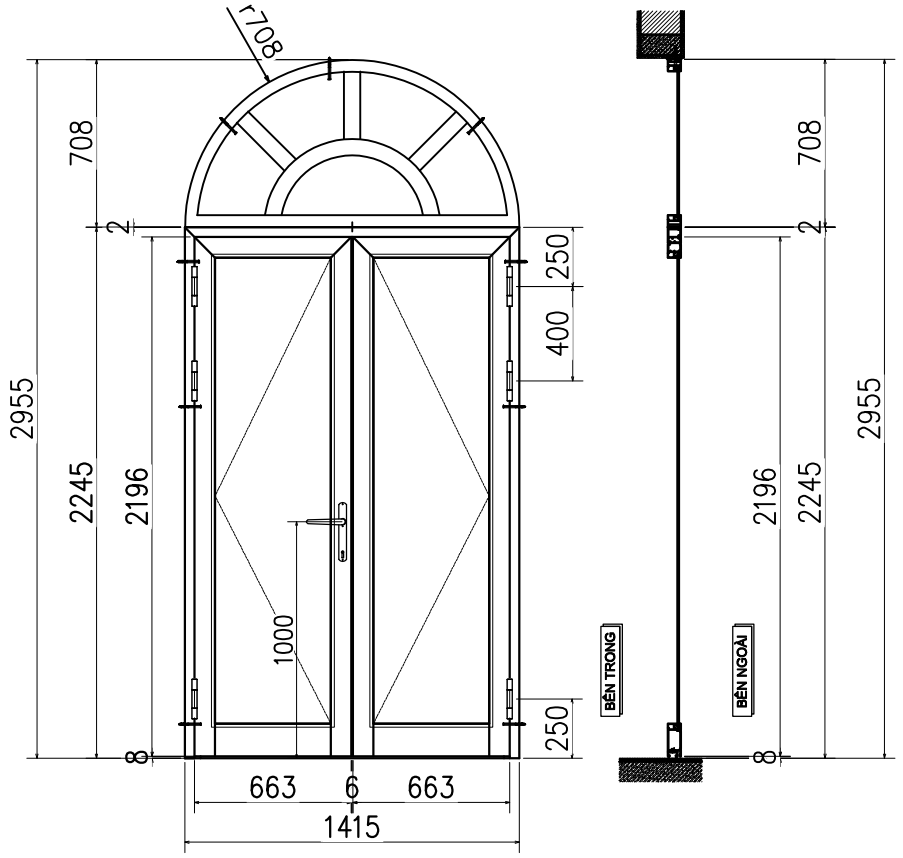

C3236

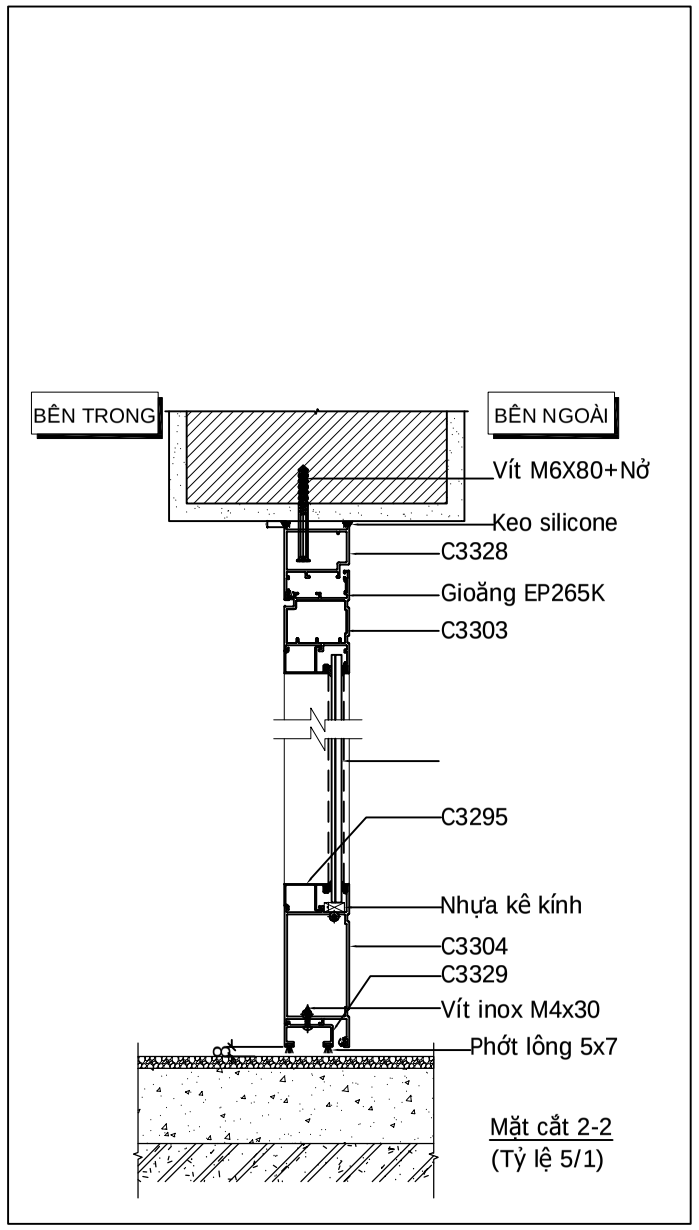

Mặt cắt 2-2
(Tỷ lệ 5/1)

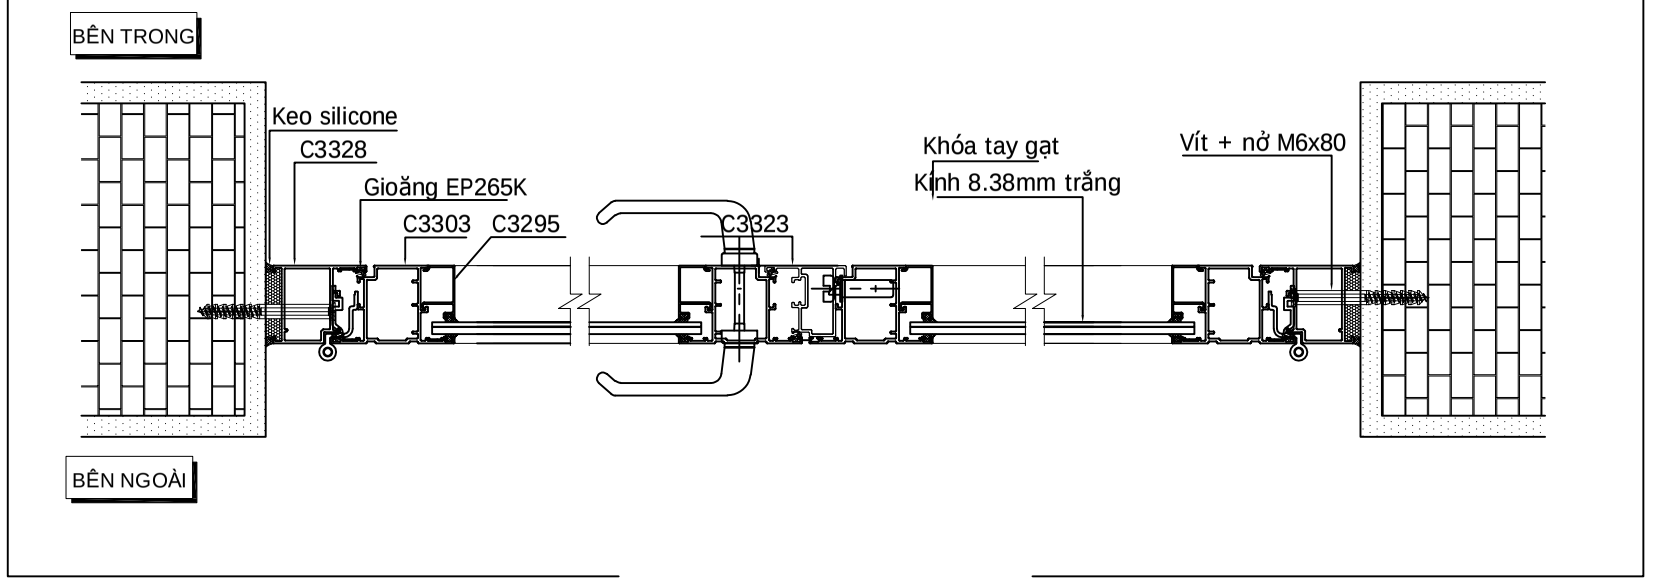

BẢNG THỐNG KÊ PHỤ KIỆN- KHÓA ĐA ĐIỂM			
Phụ kiện	Mã phụ kiện	Số lượng	Ghi chú
Bản lề bi đũa		6 cái	
Tay khoá		1 cái	
Thân khoá		1 cái	ĐA ĐIỂM
Lõi khoá		1 cái	MỞ NGOÀI
Thanh CĐ		1 cái	
Vấu khóa		2 cái	
Chốt âm ngắn		1 cái	
Chốt âm dài		1 cái	
Hố chốt		1 cái	

D1T2-1 SL: 01 BỘ	QUY CÁCH	CỬA SỔ MỞ QUAY 1 CÁNH LIỀN VÁCH KÍNH
	HỆ NHÔM	XINGFA 55
	KÍNH	hộp 19 trong
	SƠN	TĨNH ĐIỆN THEO MÀU PHÊ DUYỆT
VỊ TRÍ LẮP ĐẶT	PHỤ KIỆN	DAISHIN
	GHI CHÚ	HƯỚNG NHÌN TỪ BÊN NGOÀI

CHỦ ĐẦU TƯ - INVESTOR:

XÁC NHẬN CỦA TVGS & TVTK:

DỰ ÁN - PROJECT:

GÓI THẦU:
CUNG CẤP SẢN XUẤT VÀ THI CÔNG LẮP ĐẶT PHẦN CỬA ĐI, CỬA SỔ, VÁCH NHÔM KÍNH

NHÀ THẦU:
CÔNG TY CỔ NHÔM AN PHÚ
Địa chỉ: Thôn Khê Nữ - X. Phúc Thịnh - TP. Hà Nội

Chủ trì: Project manager:	
Kiểm tra: check by:	
Thiết kế: design by:	Ks. Đặng Anh Dũng


TÊN BẢN VẼ - NAME DRAWING:

Sửa đổi


Lần/rev	Ngày/date	Xác nhận/confirm

Bản vẽ số/ drawing:
Ngày tháng/date:


GHI CHÚ:
-KÍCH THƯỚC SẢN XUẤT LÀ KÍCH THƯỚC ĐỂ GIA CÔNG CỬA THÀNH PHẨM
-CHIỀU MỞ CỬA TỪNG VỊ TRÍ XEM TRÊN BẢN VẼ MẶT BẰNG
-KHOAN LỖ THOÁT NƯỚC MƯA VÀ LỖ LẮP ĐẶT TRƯỚC KHI RA CÔNG TRƯỜNG

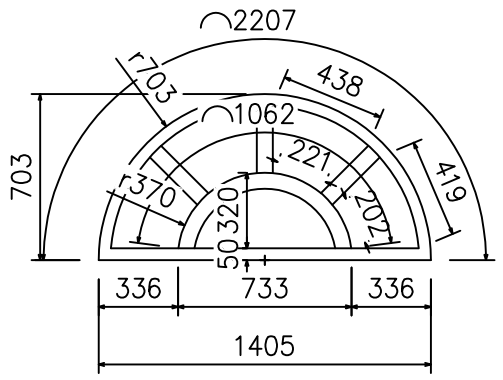


KH: D1T2-2
SL: 01
C3209+C3236=2750
C3203+C3236=1600

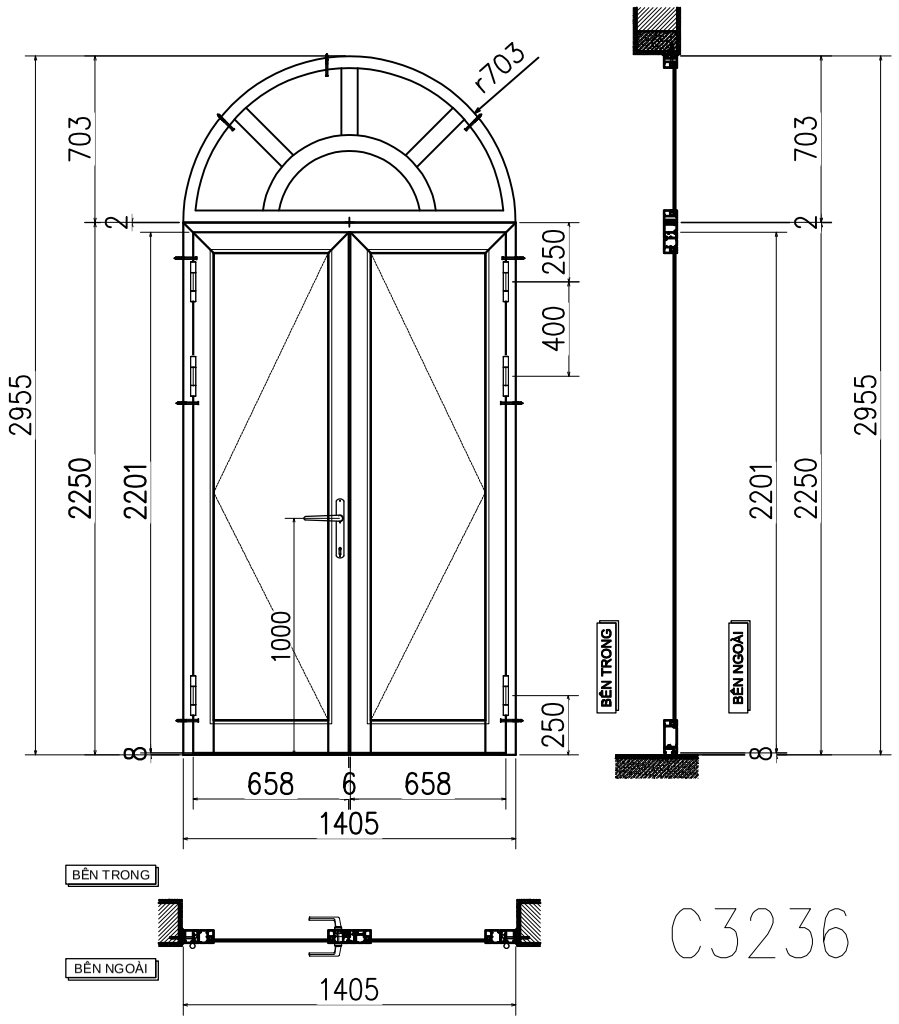

C3236

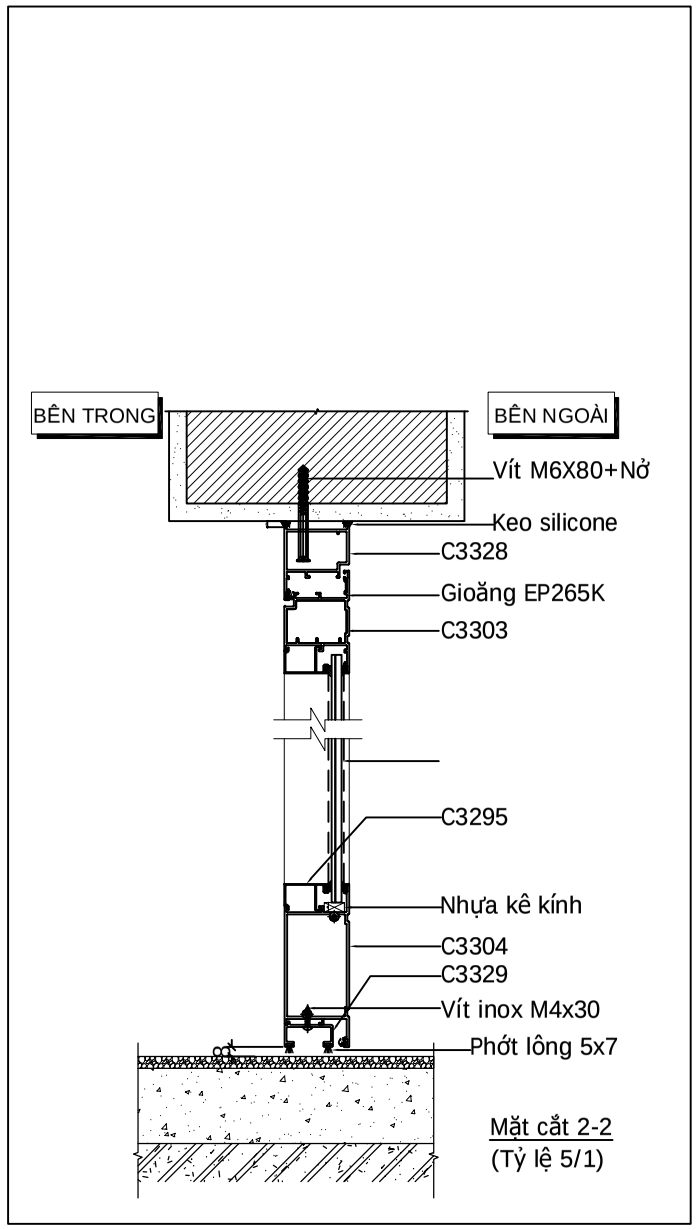

Mặt cắt 2-2
(Tỷ lệ 5/1)

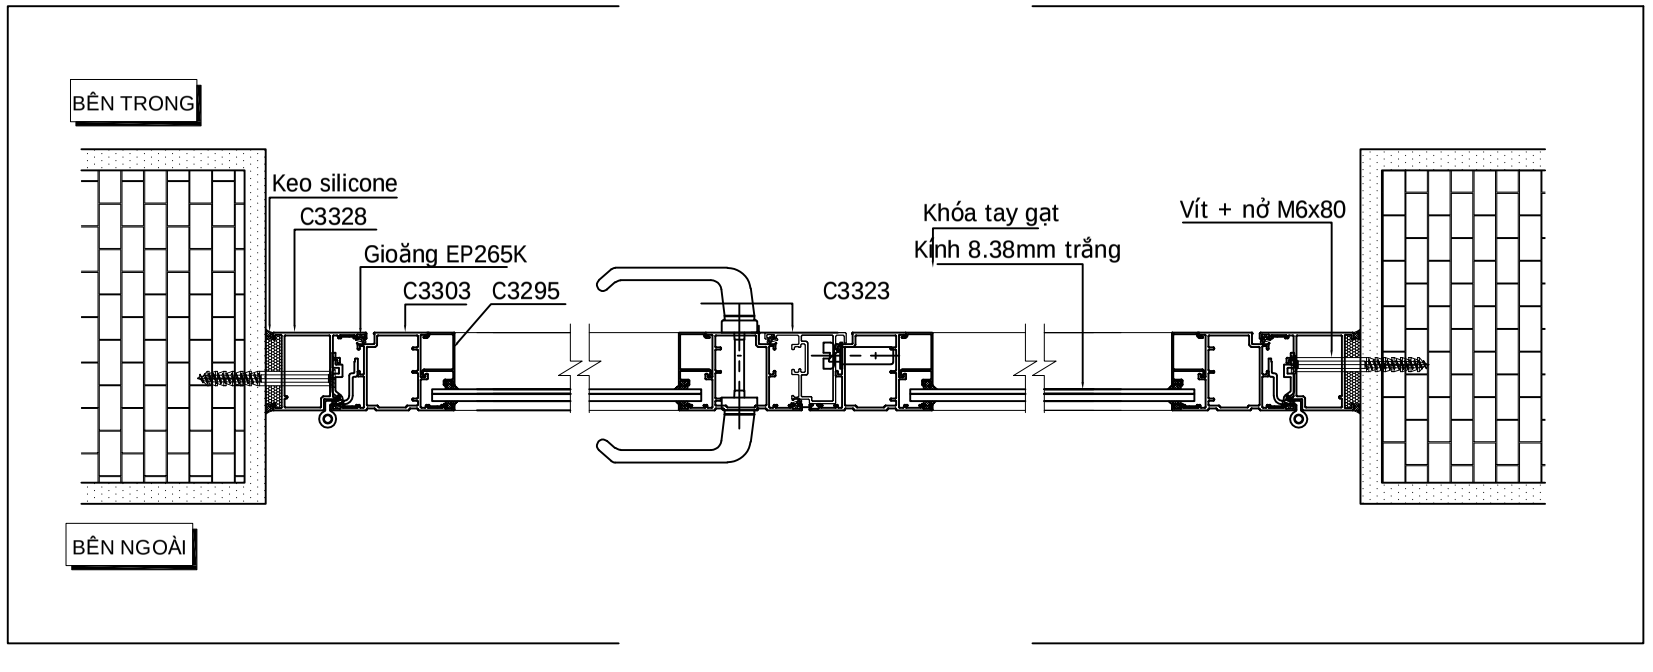

BẢNG THỐNG KÊ PHỤ KIỆN- KHÓA ĐA ĐIỂM			
Phụ kiện	Mã phụ kiện	Số lượng	Ghi chú
Bản lề bi đũa		6 cái	
Tay khoá		1 cái	
Thân khoá		1 cái	ĐA ĐIỂM
Lõi khoá		1 cái	MỞ NGOÀI
Thanh CĐ		1 cái	
Vấu khóa		2 cái	
Chốt âm ngắn		1 cái	
Chốt âm dài		1 cái	
Hố chốt		1 cái	

D1T2-2 SL: 01 BỘ	QUY CÁCH	CỬA SỔ MỞ QUAY 1 CÁNH LIỀN VÁCH KÍNH
	HỆ NHÔM	XINGFA 55
	KÍNH	hộp 19 trong
	SƠN	TĨNH ĐIỆN THEO MÀU PHÊ DUYỆT
VỊ TRÍ LẮP ĐẶT	PHỤ KIỆN	DAISHIN
	GHI CHÚ	HƯỚNG NHÌN TỪ BÊN NGOÀI

CHỦ ĐẦU TƯ - INVESTOR:

XÁC NHẬN CỦA TVGS & TVTK:

DỰ ÁN - PROJECT:

GÓI THẦU:
CUNG CẤP SẢN XUẤT VÀ THI CÔNG LẮP ĐẶT PHẦN CỬA ĐI, CỬA SỔ, VÁCH NHÔM KÍNH

NHÀ THẦU:
CÔNG TY CỔ NHÔM AN PHÚ
Địa chỉ: Thôn Khê Nữ - X. Phúc Thịnh - TP. Hà Nội

Chủ trì: Project manager:	
Kiểm tra: check by:	
Thiết kế: design by:	Ks. Đặng Anh Dũng

TÊN BẢN VẼ - NAME DRAWING:


Sửa đổi

Lần/rev	Ngày/date	Xác nhận/confirm


Bản vẽ số/ drawing:

Ngày tháng/date:


GHI CHÚ:
-KÍCH THƯỚC SẢN XUẤT LÀ KÍCH THƯỚC ĐỂ GIA CÔNG CỬA THÀNH PHẨM
-CHIỀU MỞ CỬA TỪNG VỊ TRÍ XEM TRÊN BẢN VẼ MẶT BẰNG
-KHOAN LỖ THOÁT NƯỚC MƯA VÀ LỖ LẮP ĐẶT TRƯỚC KHI RA CÔNG TRƯỜNG

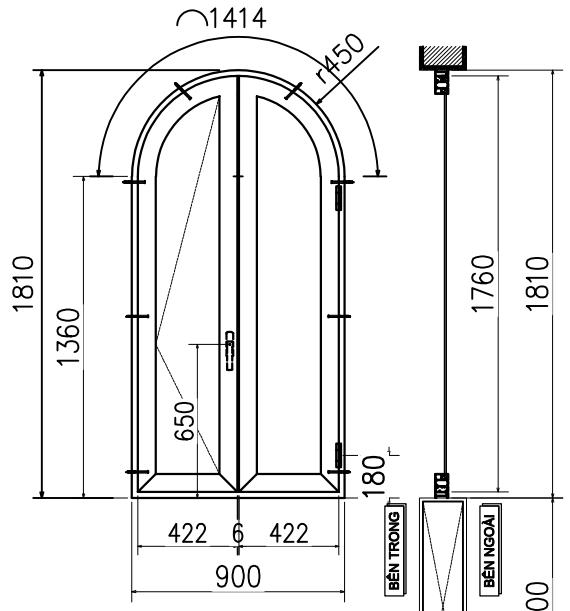


KH: S3T2
SL: 01
C3318+C3296=4600

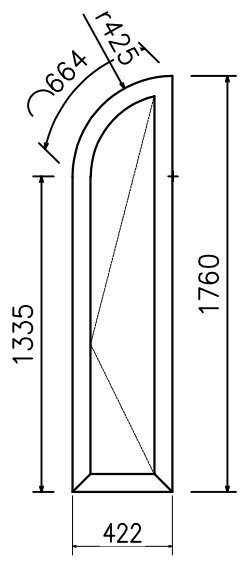


KH: S3T2
ĐỐI XỨNG
C3202+C3236=2500*2

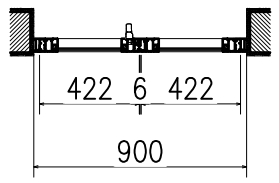

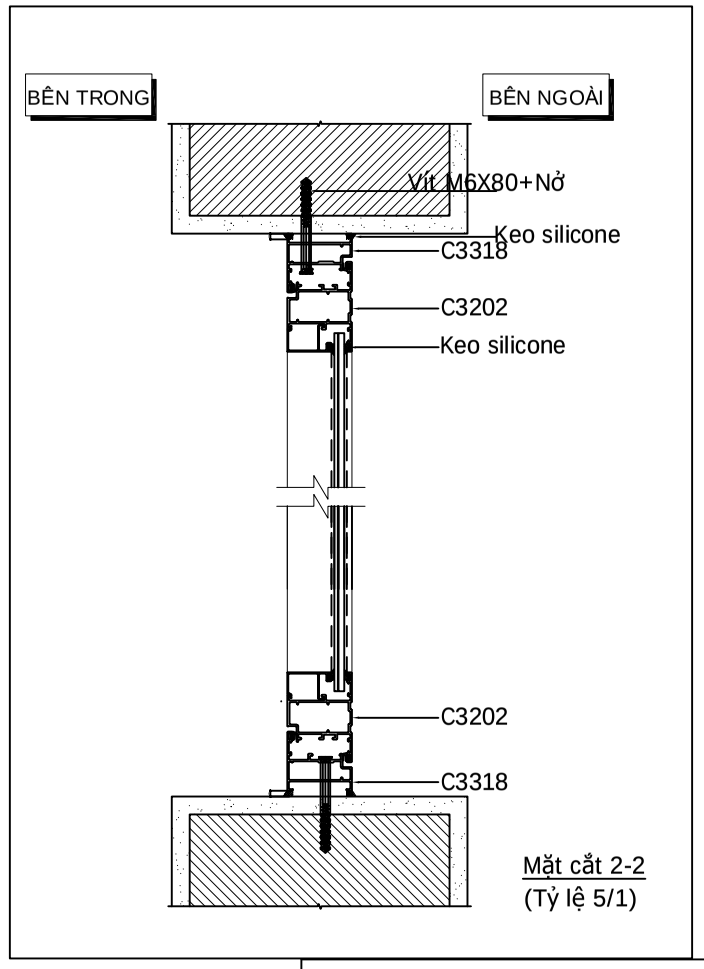

Mặt cắt 2-2
(Tỷ lệ 5/1)

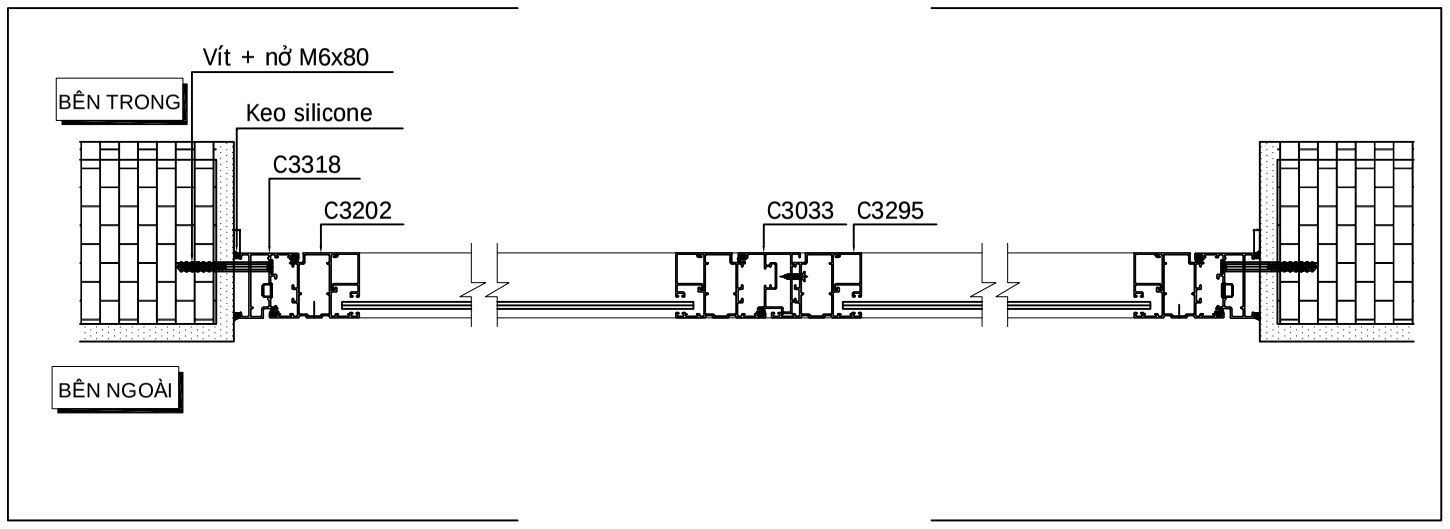

BẢNG THỐNG KÊ PHỤ KIỆN CS2 CÁNH			
Phụ kiện	Mã phụ kiện	Số lượng	Ghi chú
Bản 1D		4 cái	
Tay khoá		1 cái	Màu bạc
Thanh CĐ		1 cái	
Vấu khóa		2 cái	
Chốt âm dài		1 cái	
Chốt âm ngắn		1 cái	
Hố chốt		1 cái	
đệm chống xệ		2 bộ	
Nhựa bịt đố		1 bộ	

S3T2	QUY CÁCH	CỬA SỔ MỞ QUAY 1 CÁNH LIỀN VÁCH KÍNH
SL: 01 BỘ	HỆ NHÔM	XINGFA 55
	KÍNH	HỘP 19,TRONG
	SƠN	TĨNH ĐIỆN THEO MÀU PHÊ DUYỆT
VỊ TRÍ LẮP ĐẶT	PHỤ KIỆN	DAISHIN
	GHI CHÚ	HƯỚNG NHÌN TỪ BÊN NGOÀI

CHỦ ĐẦU TƯ - INVESTOR:

XÁC NHẬN CỦA TVGS & TVTK:

DỰ ÁN - PROJECT:

GÓI THẦU:
CUNG CẤP SẢN XUẤT VÀ THI CÔNG LẮP ĐẶT PHẦN CỬA ĐI, CỬA SỔ, VÁCH NHÔM KÍNH

NHÀ THẦU:
AN PHU — ANPHU WINDOW —
CÔNG TY CỔ NHÔM AN PHÚ
Địa chỉ: Thôn Khê Nữ - X. Phúc Thịnh - TP. Hà Nội

Chủ trì: Project manager:	
Kiểm tra: check by:	
Thiết kế: design by:	Ks. Đặng Anh Dũng


TÊN BẢN VẼ - NAME DRAWING:

Sửa đổi


Lần/rev	Ngày/date	Xác nhận/confirm


Bản vẽ số/ drawing:
Ngày tháng/date:

GHI CHÚ:
-KÍCH THƯỚC SẢN XUẤT LÀ KÍCH THƯỚC ĐỂ GIA CÔNG CỬA THÀNH PHẨM
-CHIỀU MỞ CỬA TỪNG VỊ TRÍ XEM TRÊN BẢN VẼ MẶT BẰNG
-KHOAN LỖ THOÁT NƯỚC MƯA VÀ LỖ LẮP ĐẶT TRƯỚC KHI RA CÔNG TRƯỜNG

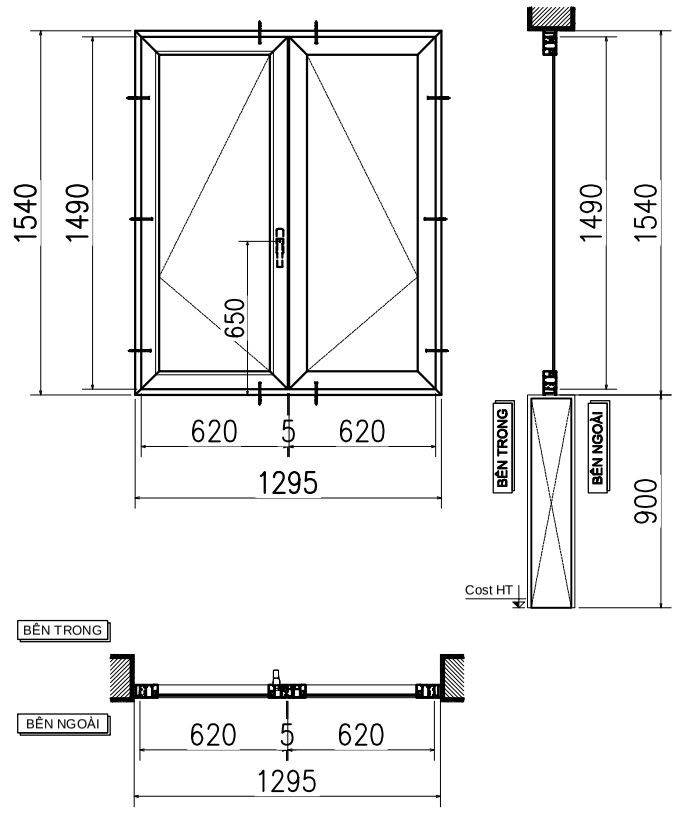

C3236

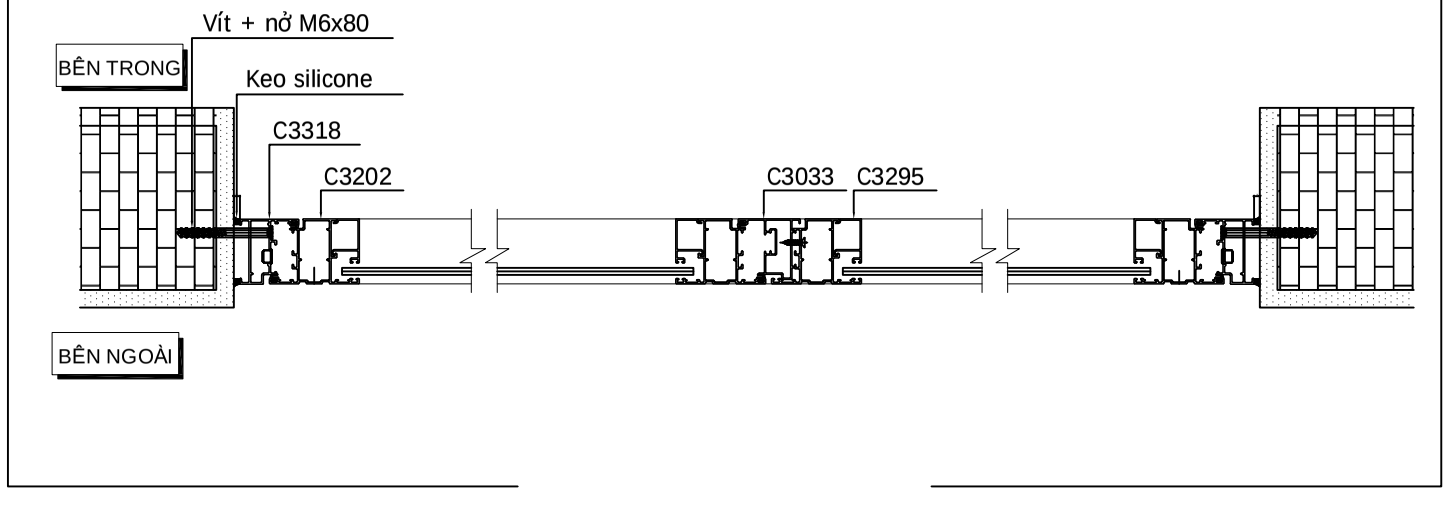

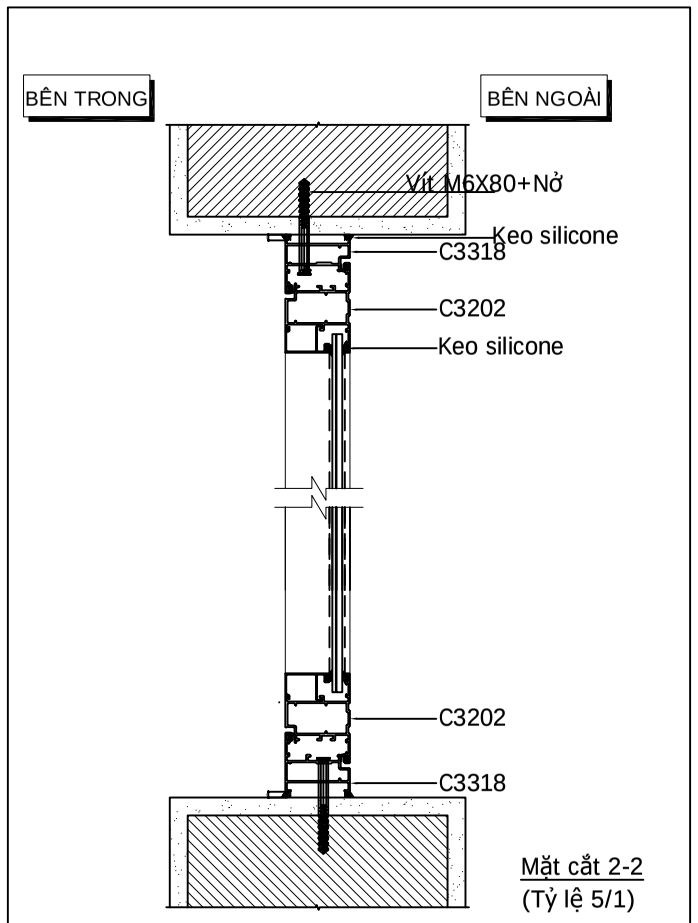

Mặt cắt 2-2
(Tỷ lệ 5/1)

BẢNG THỐNG KÊ PHỤ KIỆN CS2 CÁNH			
Phụ kiện	Mã phụ kiện	Số lượng	Ghi chú
Bản A-mở quay	14"	4 cái	
Tay khoá		1 cái	Màu bạc
Thanh CĐ		1 cái	
Vấu khóa		2 cái	
Chốt âm dài		1 cái	
Chốt âm ngắn		1 cái	
Hố chốt		1 cái	
đệm chống xệ		2 bộ	
Nhựa bịt đố		1 bộ	

S4T2 SL: 01 BỘ	QUY CÁCH	CỬA SỔ MỞ QUAY 1 CÁNH LIỀN VÁCH KÍNH
	HỆ NHÔM	XINGFA 55
	KÍNH	HỘP 19,TRONG
	SƠN	TĨNH ĐIỆN THEO MÀU PHÊ DUYỆT
VỊ TRÍ LẮP ĐẶT	PHỤ KIỆN	DAISHIN
	GHI CHÚ	HƯỚNG NHÌN TỪ BÊN NGOÀI

CHỦ ĐẦU TƯ - INVESTOR:

XÁC NHẬN CỦA TVGS & TVTK:

DỰ ÁN - PROJECT:

GÓI THẦU:
CUNG CẤP SẢN XUẤT VÀ THI CÔNG LẮP ĐẶT PHẦN CỬA ĐI, CỬA SỔ, VÁCH NHÔM KÍNH

NHÀ THẦU:
CÔNG TY CỔ NHÔM AN PHÚ
Địa chỉ: Thôn Khê Nữ - X. Phúc Thịnh - TP. Hà Nội

Chủ trì:
Project manager:

Kiểm tra:
check by:

Thiết kế:
design by: Ks. Đặng Anh Dũng

TÊN BẢN VẼ - NAME DRAWING:


Sửa đổi


Lần/rev	Ngày/date	Xác nhận/confirm

Bản vẽ số/ drawing:


Ngày tháng/date:

GHI CHÚ:
-KÍCH THƯỚC SẢN XUẤT LÀ KÍCH THƯỚC ĐỂ GIA CÔNG CỬA THÀNH PHẨM
-CHIỀU MỞ CỬA TỪNG VỊ TRÍ XEM TRÊN BẢN VẼ MẶT BẰNG
-KHOAN LỖ THOÁT NƯỚC MƯA VÀ LỖ LẮP ĐẶT TRƯỚC KHI RA CÔNG TRƯỜNG

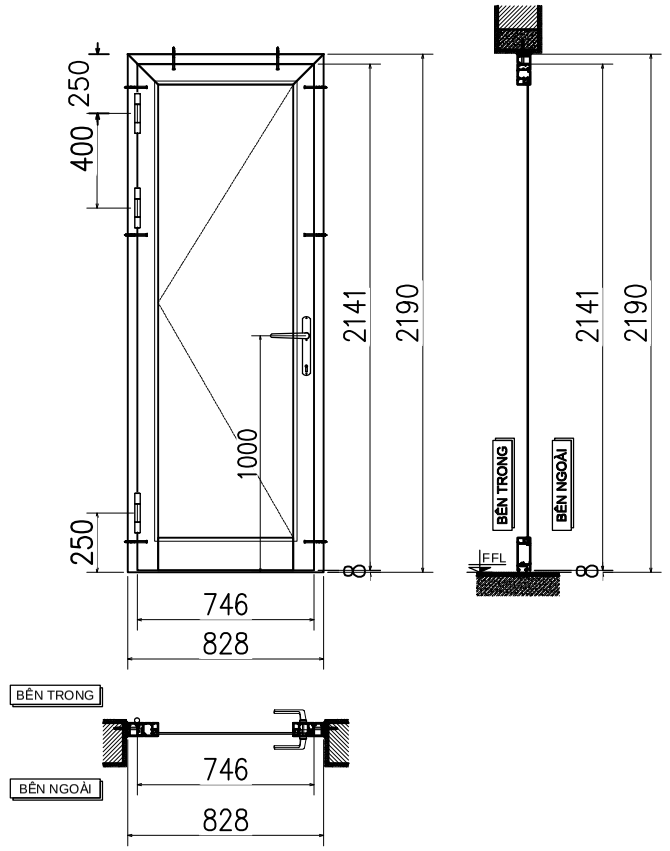

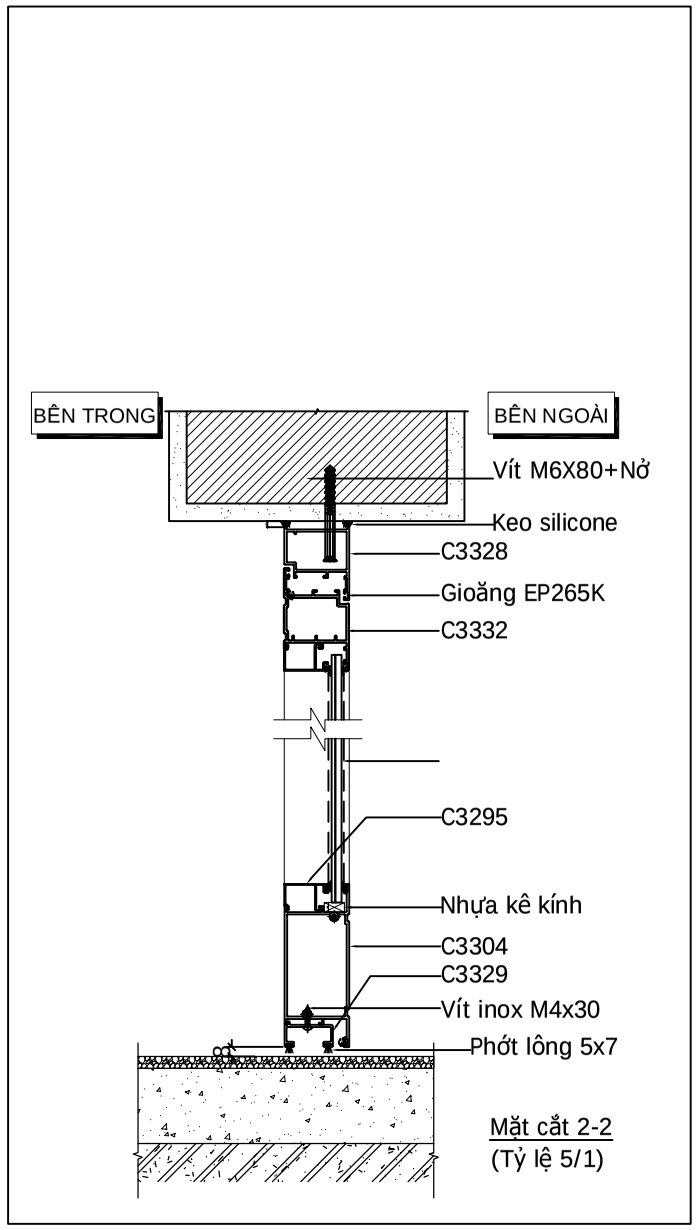

Mặt cắt 2-2
(Tỷ lệ 5/1)

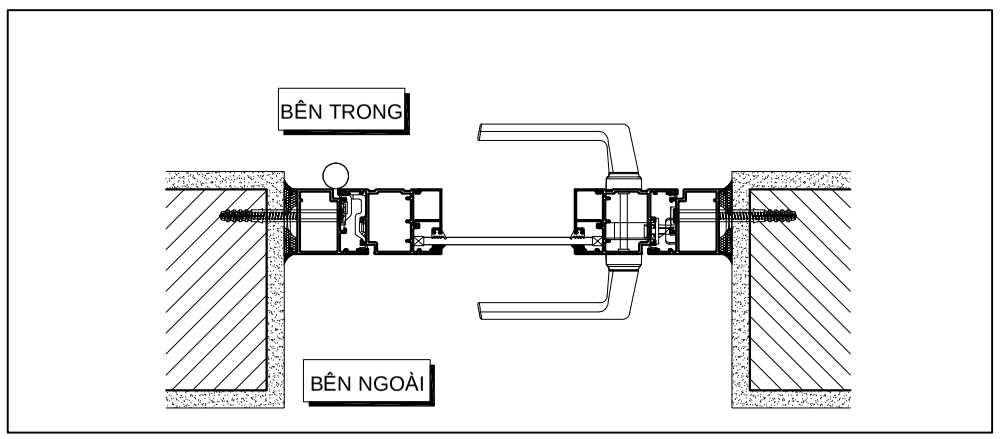

BẢNG THỐNG KÊ PHỤ KIỆN- KHÓA ĐA ĐIỂM			
Phụ kiện	Mã phụ kiện	Số lượng	Ghi chú
Bản lề bi đũa		3cái	Màu bạc
Tay khoá		1 cái	Màu bạc
Thân khoá		1 cái	Đơn ĐIỂM
Lõi khoá		1 cái	MỞ trong
		1 cái	

WCT2 SL: 01 BỘ	QUY CÁCH	CỬA SỔ MỞ QUAY 1 CÁNH LIỀN VÁCH KÍNH
	HỆ NHÔM	XINGFA 55
	KÍNH	8.38 SỮA
	SƠN	TĨNH ĐIỆN THEO MÀU PHÊ DUYỆT
VỊ TRÍ LẮP ĐẶT	PHỤ KIỆN	DAISHIN
	GHI CHÚ	HƯỚNG NHÌN TỪ BÊN NGOÀI

CHỦ ĐẦU TƯ - INVESTOR:

XÁC NHẬN CỦA TVGS & TVTK:

DỰ ÁN - PROJECT:

GÓI THẦU:
CUNG CẤP SẢN XUẤT VÀ THI CÔNG LẮP ĐẶT PHẦN CỬA ĐI, CỬA SỔ, VÁCH NHÔM KÍNH

NHÀ THẦU:
AN PHU — ANPHU WINDOW —
CÔNG TY CỔ NHÔM AN PHÚ
Địa chỉ: Thôn Khê Nữ - X. Phúc Thịnh - TP. Hà Nội

Chủ trì: Project manager:	
Kiểm tra: check by:	
Thiết kế: design by:	Ks. Đặng Anh Dũng


TÊN BẢN VẼ - NAME DRAWING:

Sửa đổi

Lần/rev	Ngày/date	Xác nhận/confirm


Bản vẽ số/ drawing:	
Ngày tháng/date:	


GHI CHÚ:
-KÍCH THƯỚC SẢN XUẤT LÀ KÍCH THƯỚC ĐỂ GIA CÔNG CỬA THÀNH PHẨM
-CHIỀU MỞ CỬA TỪNG VỊ TRÍ XEM TRÊN BẢN VẼ MẶT BẰNG
-KHOAN LỖ THOÁT NƯỚC MƯA VÀ LỖ LẮP ĐẶT TRƯỚC KHI RA CÔNG TRƯỜNG

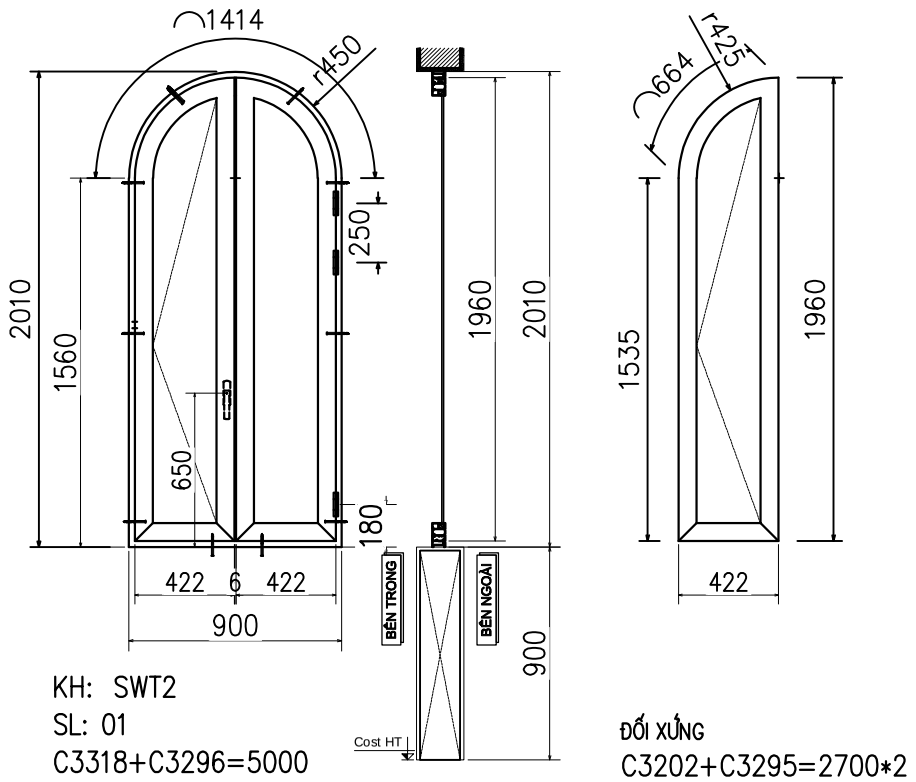


KH: SWT2
SL: 01
C3318+C3296=5000

ĐỐI XỨNG
C3202+C3295=2700*2

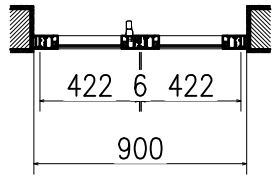

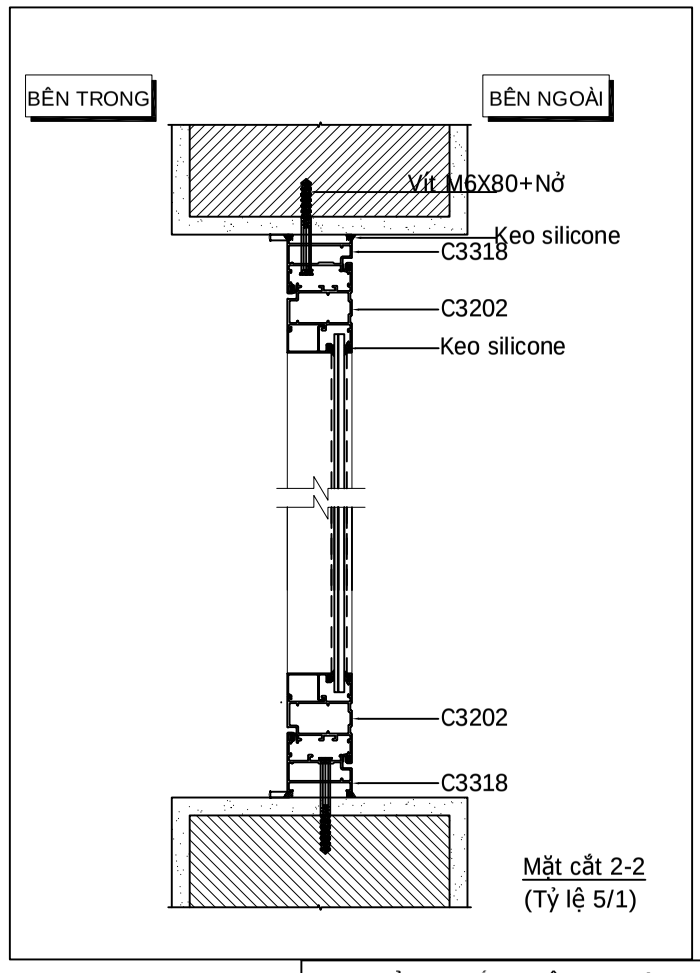

Mặt cắt 2-2
(Tỷ lệ 5/1)

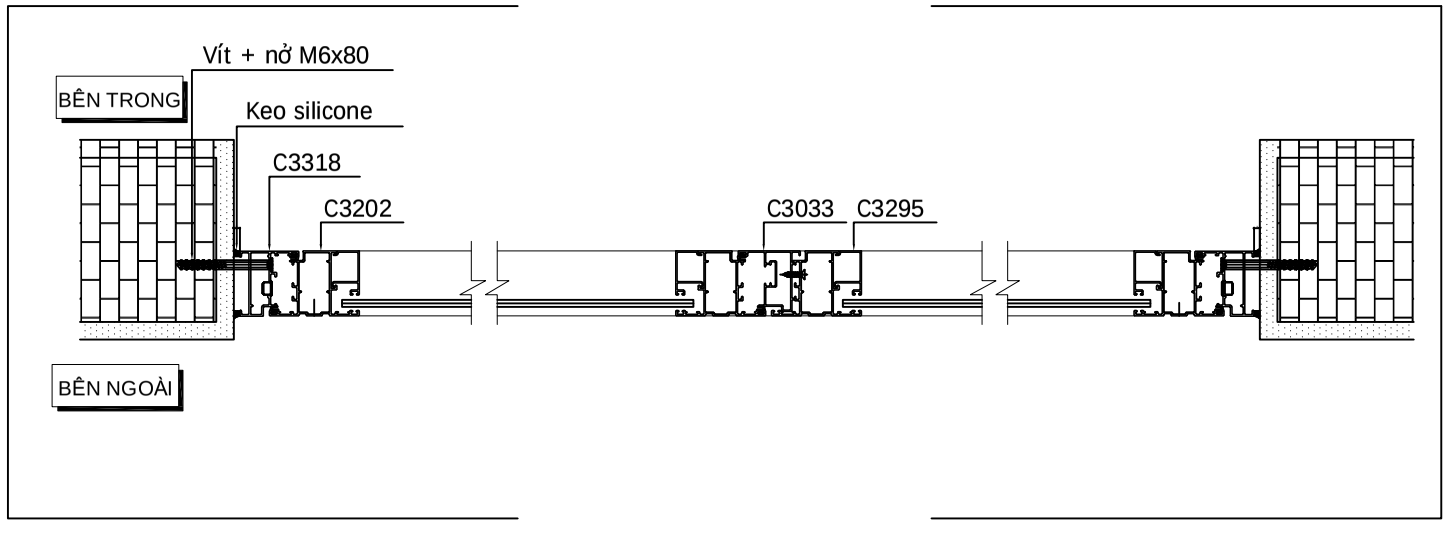

BẢNG THỐNG KÊ PHỤ KIỆN CS2 CÁNH			
Phụ kiện	Mã phụ kiện	Số lượng	Ghi chú
Bản 1D		6 cái	
Tay khoá		1 cái	Màu bạc
Thanh CĐ		1 cái	
Vấu khóa		2 cái	
Chốt âm dài		1 cái	
Chốt âm ngắn		1 cái	
Hố chốt		1 cái	
đệm chống xệ		2 bộ	
Nhựa bịt đố		1 bộ	

SwT2 SL: 01 BỘ	QUY CÁCH	CỬA SỔ MỞ QUAY 1 CÁNH LIỀN VÁCH KÍNH
	HỆ NHÔM	XINGFA 55
	KÍNH	8.38 sữa
	SƠN	TĨNH ĐIỆN THEO MÀU PHÊ DUYỆT
VỊ TRÍ LẮP ĐẶT	PHỤ KIỆN	DAISHIN
	GHI CHÚ	HƯỚNG NHÌN TỪ BÊN NGOÀI

CHỦ ĐẦU TƯ - INVESTOR:

XÁC NHẬN CỦA TVGS & TVTK:

DỰ ÁN - PROJECT:

GÓI THẦU:
CUNG CẤP SẢN XUẤT VÀ THI CÔNG LẮP ĐẶT PHẦN CỬA ĐI, CỬA SỔ, VÁCH NHÔM KÍNH

NHÀ THẦU:
CÔNG TY CỔ NHÔM AN PHÚ
Địa chỉ: Thôn Khê Nữ - X. Phúc Thịnh - TP. Hà Nội

Chủ trì: Project manager:	
Kiểm tra: check by:	
Thiết kế: design by:	Ks. Đặng Anh Dũng

TÊN BẢN VẼ - NAME DRAWING:


Sửa đổi

Lần/rev	Ngày/date	Xác nhận/confirm

Bản vẽ số/ drawing:


Ngày tháng/date:

GHI CHÚ:
-KÍCH THƯỚC SẢN XUẤT LÀ KÍCH THƯỚC ĐỂ GIA CÔNG CỬA THÀNH PHẨM
-CHIỀU MỞ CỬA TỪNG VỊ TRÍ XEM TRÊN BẢN VẼ MẶT BẰNG
-KHOAN LỖ THOÁT NƯỚC MƯA VÀ LỖ LẮP ĐẶT TRƯỚC KHI RA CÔNG TRƯỜNG

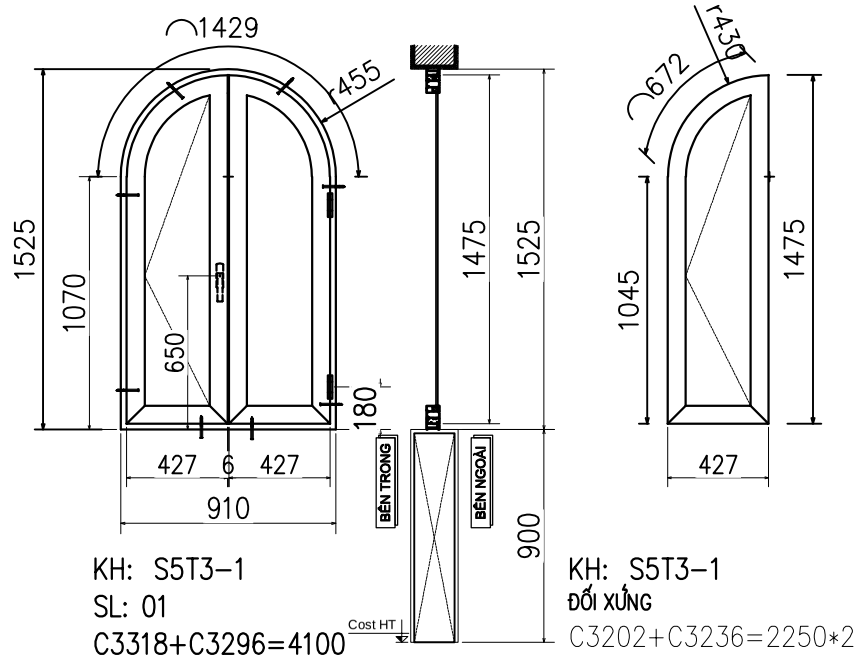


KH: S5T3-1
SL: 01
C3318+C3296=4100


KH: S5T3-1
ĐỐI XỨNG
C3202+C3236=2250*2

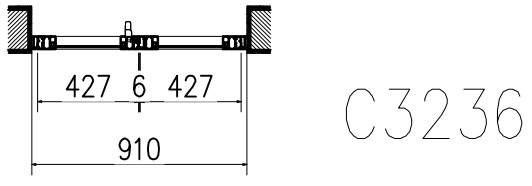

C3236

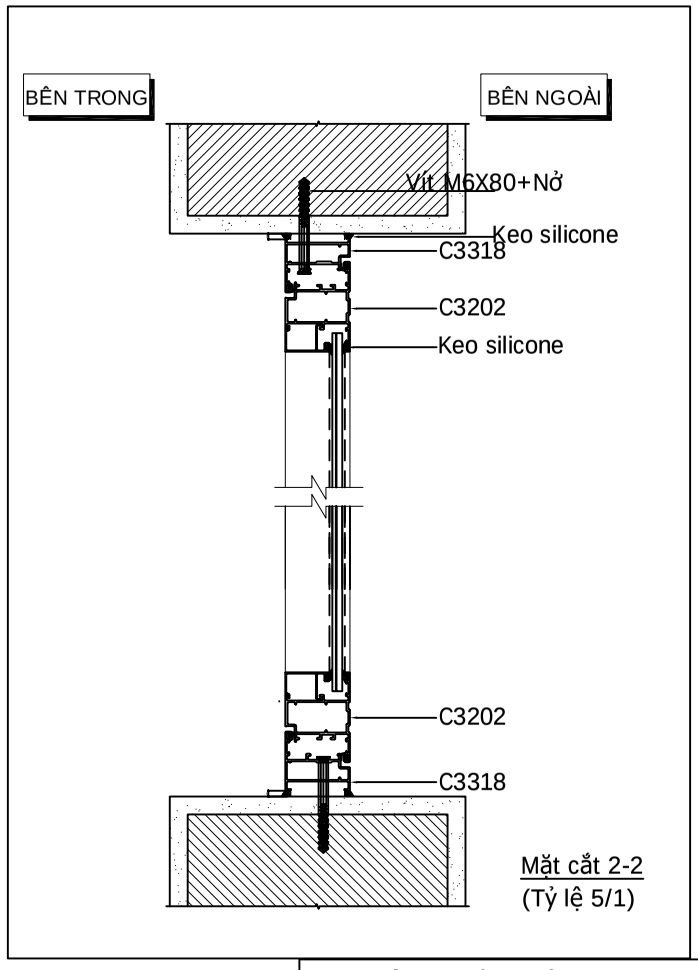

Mặt cắt 2-2
(Tỷ lệ 5/1)

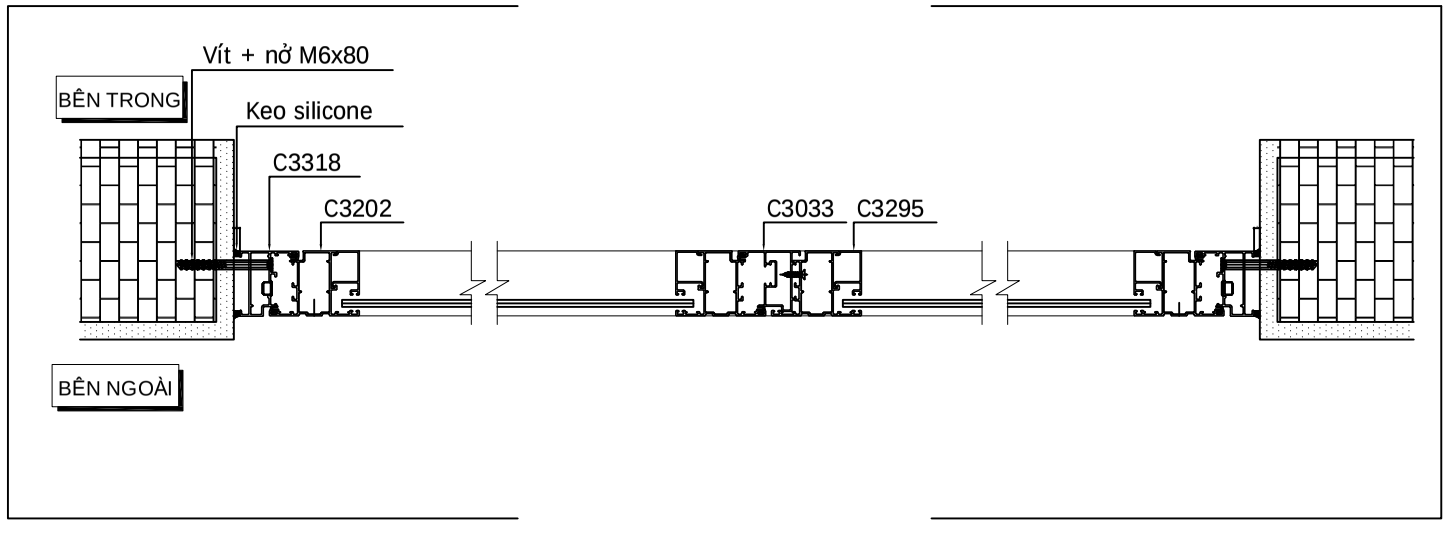

BẢNG THỐNG KÊ PHỤ KIỆN CS2 CÁNH

Phụ kiện	Mã phụ kiện	Số lượng	Ghi chú
Bản 1D		4 cái	
Tay khoá		1 cái	Màu bạc
Thanh CĐ		1 cái	
Vấu khóa		2 cái	
Chốt âm dài		1 cái	
Chốt âm ngắn		1 cái	
Hố chốt		1 cái	
đệm chống xệ		2 bộ	
Nhựa bịt đố		1 bộ	

KH:			
	S5T3-1	QUY CÁCH	CỬA SỔ MỞ QUAY 1 CÁNH LIỀN VÁCH KÍNH
	SL: 01 BỘ	HỆ NHÔM	XINGFA 55
		KÍNH	HỘP 19,TRONG
		SƠN	TĨNH ĐIỆN THEO MÀU PHÊ DUYỆT
	VỊ TRÍ LẮP ĐẶT	PHỤ KIỆN	DAISHIN
		GHI CHÚ	HƯỚNG NHÌN TỪ BÊN NGOÀI

CHỦ ĐẦU TƯ - INVESTOR:

XÁC NHẬN CỦA TVGS & TVTK:

DỰ ÁN - PROJECT:

GÓI THẦU:
CUNG CẤP SẢN XUẤT VÀ THI CÔNG LẮP ĐẶT PHẦN CỬA ĐI, CỬA SỔ, VÁCH NHÔM KÍNH

NHÀ THẦU:
AN PHU — ANPHU WINDOW —
CÔNG TY CỔ NHÔM AN PHÚ
Địa chỉ: Thôn Khê Nữ - X. Phúc Thịnh - TP. Hà Nội

Chủ trì: Project manager:	
Kiểm tra: check by:	
Thiết kế: design by:	Ks. Đặng Anh Dũng

TÊN BẢN VẼ - NAME DRAWING:


Sửa đổi

Lần/rev	Ngày/date	Xác nhận/confirm

Bản vẽ số/ drawing:


Ngày tháng/date:

GHI CHÚ:
-KÍCH THƯỚC SẢN XUẤT LÀ KÍCH THƯỚC ĐỂ GIA CÔNG CỬA THÀNH PHẨM
-CHIỀU MỞ CỬA TỪNG VỊ TRÍ XEM TRÊN BẢN VẼ MẶT BẰNG
-KHOAN LỖ THOÁT NƯỚC MƯA VÀ LỖ LẮP ĐẶT TRƯỚC KHI RA CÔNG TRƯỜNG

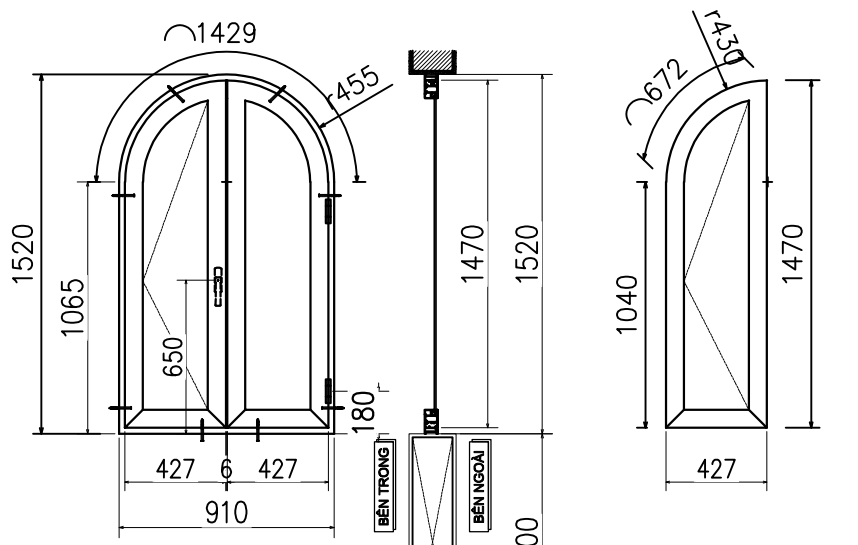


KH: S5T3-2
SL: 01
C3318+C3296=4100


KH: S5T3-2
ĐỐI XỨNG
C3202+C3236=2250*2

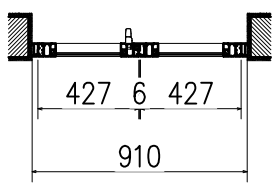

C3236

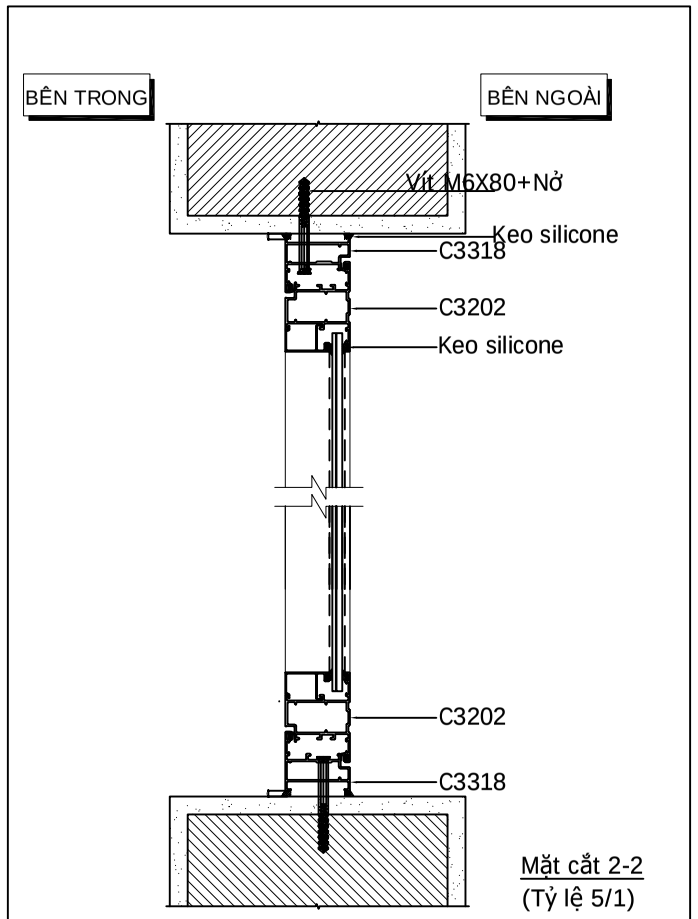

Mặt cắt 2-2
(Tỷ lệ 5/1)

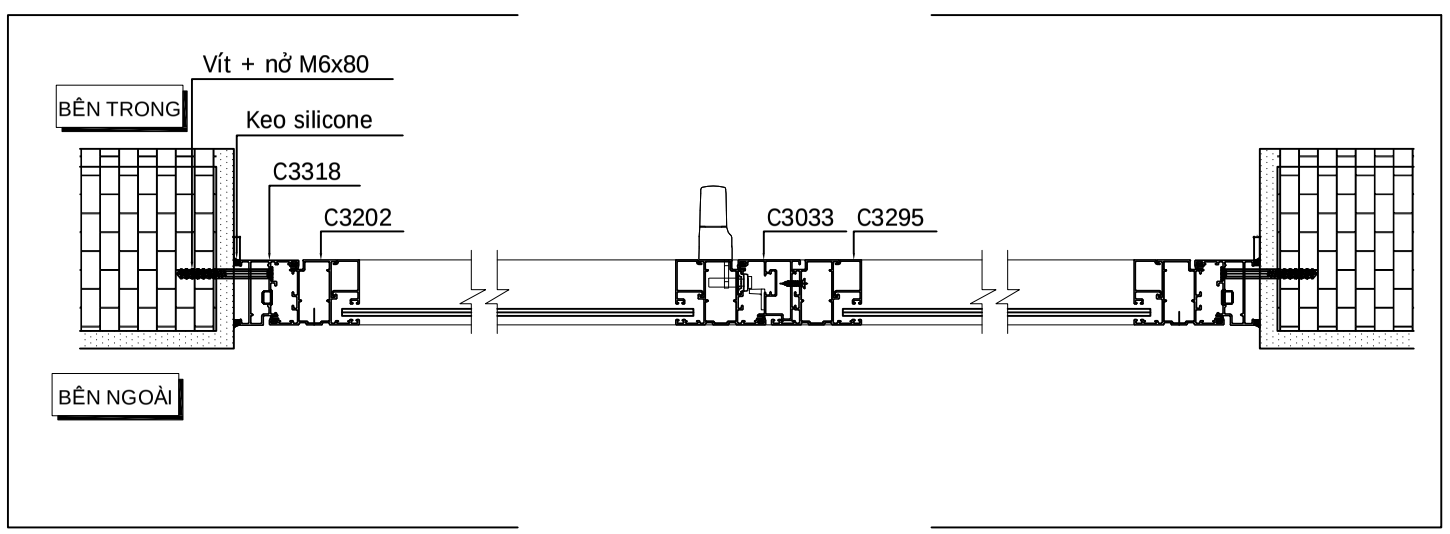

BẢNG THỐNG KÊ PHỤ KIỆN CS2 CÁNH			
Phụ kiện	Mã phụ kiện	Số lượng	Ghi chú
Bản 1D		4 cái	
Tay khoá		1 cái	Màu bạc
Thanh CĐ		1 cái	
Vấu khóa		2 cái	
Chốt âm dài		1 cái	
Chốt âm ngắn		1 cái	
Hố chốt		1 cái	
đệm chống xệ		2 bộ	
Nhựa bịt đố		1 bộ	

KH:	S5T3-2		
	SL: 01 BỘ	QUY CÁCH	CỬA SỔ MỞ QUAY 1 CÁNH LIỀN VÁCH KÍNH
		HỆ NHÔM	XINGFA 55
		KÍNH	HỘP 19,TRONG
		SƠN	TĨNH ĐIỆN THEO MÀU PHÊ DUYỆT
	VỊ TRÍ LẮP ĐẶT	PHỤ KIỆN	DAISHIN
		GHI CHÚ	HƯỚNG NHÌN TỪ BÊN NGOÀI

CHỦ ĐẦU TƯ - INVESTOR:

XÁC NHẬN CỦA TVGS & TVTK:

DỰ ÁN - PROJECT:

GÓI THẦU:
CUNG CẤP SẢN XUẤT VÀ THI CÔNG LẮP ĐẶT PHẦN CỬA ĐI, CỬA SỔ, VÁCH NHÔM KÍNH

NHÀ THẦU:
CÔNG TY CỔ NHÔM AN PHÚ
Địa chỉ: Thôn Khê Nữ - X. Phúc Thịnh - TP. Hà Nội

Chủ trì: Project manager:	
Kiểm tra: check by:	
Thiết kế: design by:	Ks. Đặng Anh Dũng

TÊN BẢN VẼ - NAME DRAWING:


Sửa đổi


Lần/rev	Ngày/date	Xác nhận/confirm


Bản vẽ số/ drawing:

Ngày tháng/date:

GHI CHÚ:
-KÍCH THƯỚC SẢN XUẤT LÀ KÍCH THƯỚC ĐỂ GIA CÔNG CỬA THÀNH PHẨM
-CHIỀU MỞ CỬA TỪNG VỊ TRÍ XEM TRÊN BẢN VẼ MẶT BẰNG
-KHOAN LỖ THOÁT NƯỚC MƯA VÀ LỖ LẮP ĐẶT TRƯỚC KHI RA CÔNG TRƯỜNG

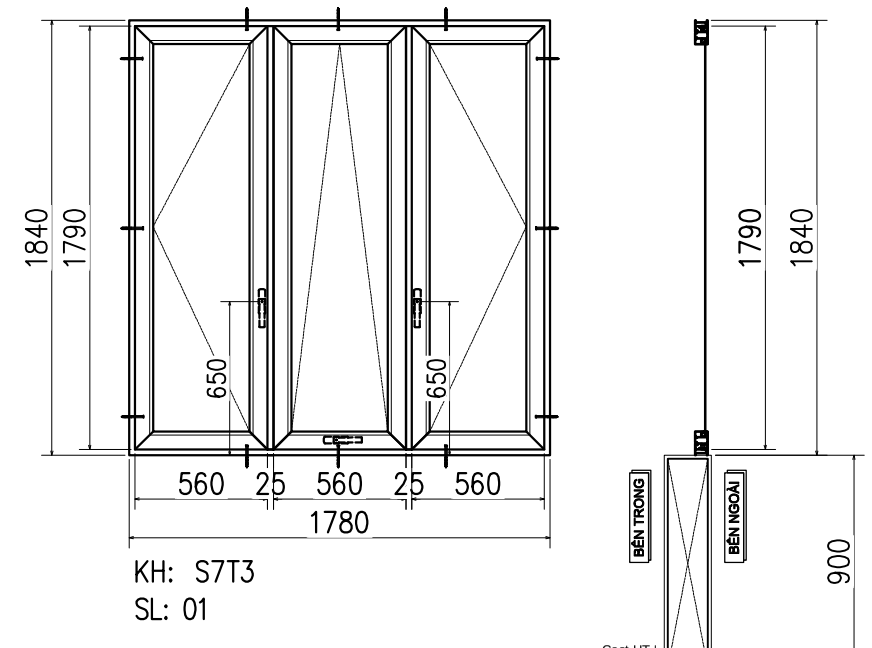

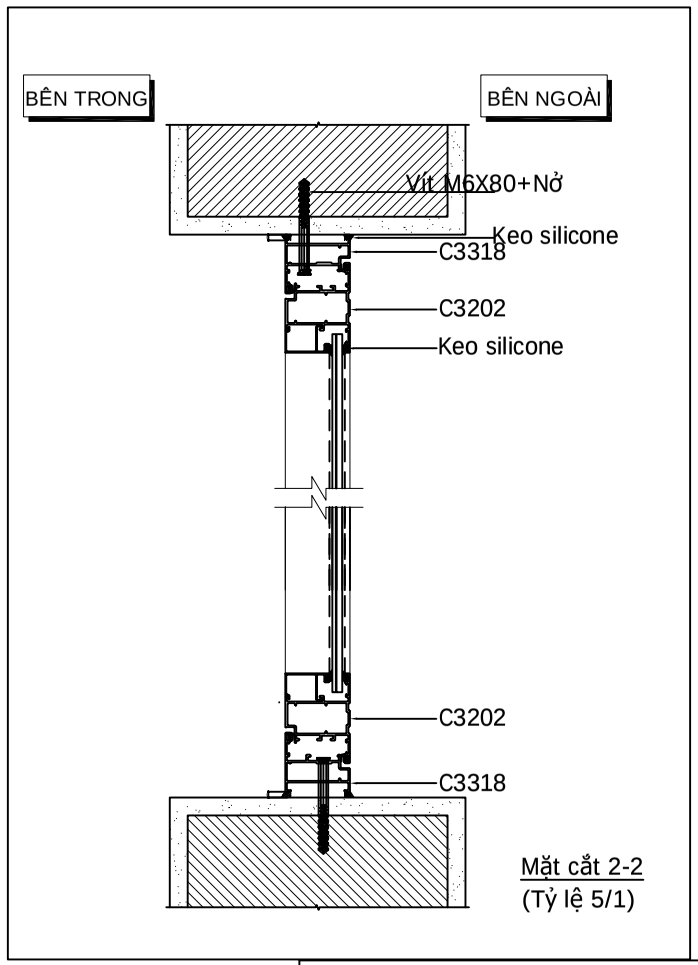

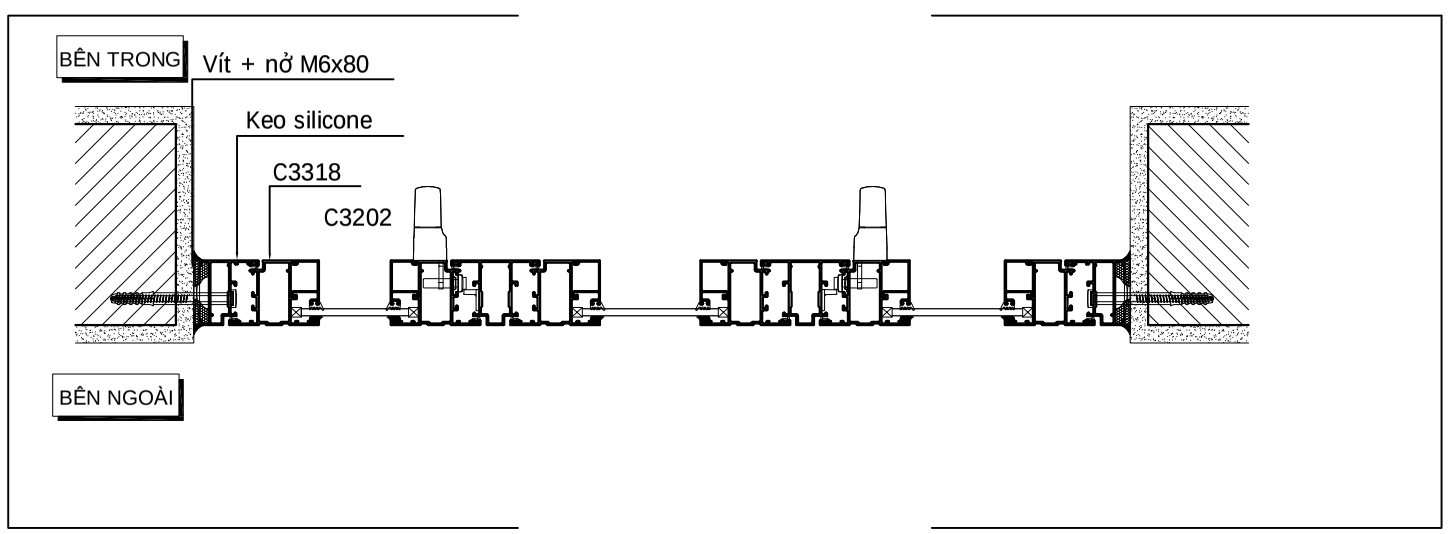

BẢNG THỐNG KÊ PHỤ KIỆN CS2 CÁNH			
Phụ kiện	Mã phụ kiện	Số lượng	Ghi chú
Bản A-mở quay	14"	4 cái	
Tay khoá		3 cái	Màu bạc
Thanh CĐ		3 cái	
Vấu khóa		6 cái	
Bản A-mở HẤT	14"	2 cái	
CHỐNG SAO	12"	2 cái	
		1 cái	
đệm chống xệ		4 bộ	
		1 bộ	

KH: S7T3		
SL: 01 BỘ	QUY CÁCH	CỬA SỔ MỞ QUAY 1 CÁNH LIỀN VÁCH KÍNH
	HỆ NHÔM	XINGFA 55
	KÍNH	HỘP 19,TRONG
	SƠN	TĨNH ĐIỆN THEO MÀU PHÊ DUYỆT
VỊ TRÍ LẮP ĐẶT	PHỤ KIỆN	DAISHIN
	GHI CHÚ	HƯỚNG NHÌN TỪ BÊN NGOÀI

CHỦ ĐẦU TƯ - INVESTOR:

XÁC NHẬN CỦA TVGS & TVTK:

DỰ ÁN - PROJECT:

GÓI THẦU:
CUNG CẤP SẢN XUẤT VÀ THI CÔNG LẮP ĐẶT PHẦN CỬA ĐI, CỬA SỔ, VÁCH NHÔM KÍNH

NHÀ THẦU:
CÔNG TY CỔ NHÔM AN PHÚ
Địa chỉ: Thôn Khê Nữ - X. Phúc Thịnh - TP. Hà Nội

Chủ trì: Project manager:	
Kiểm tra: check by:	
Thiết kế: design by:	Ks. Đặng Anh Dũng


TÊN BẢN VẼ - NAME DRAWING:

Sửa đổi

Lần/rev	Ngày/date	Xác nhận/confirm


Bản vẽ số/ drawing:	
Ngày tháng/date:	


GHI CHÚ:
-KÍCH THƯỚC SẢN XUẤT LÀ KÍCH THƯỚC ĐỂ GIA CÔNG CỬA THÀNH PHẨM
-CHIỀU MỞ CỬA TỪNG VỊ TRÍ XEM TRÊN BẢN VẼ MẶT BẰNG
-KHOAN LỖ THOÁT NƯỚC MƯA VÀ LỖ LẮP ĐẶT TRƯỚC KHI RA CÔNG TRƯỜNG

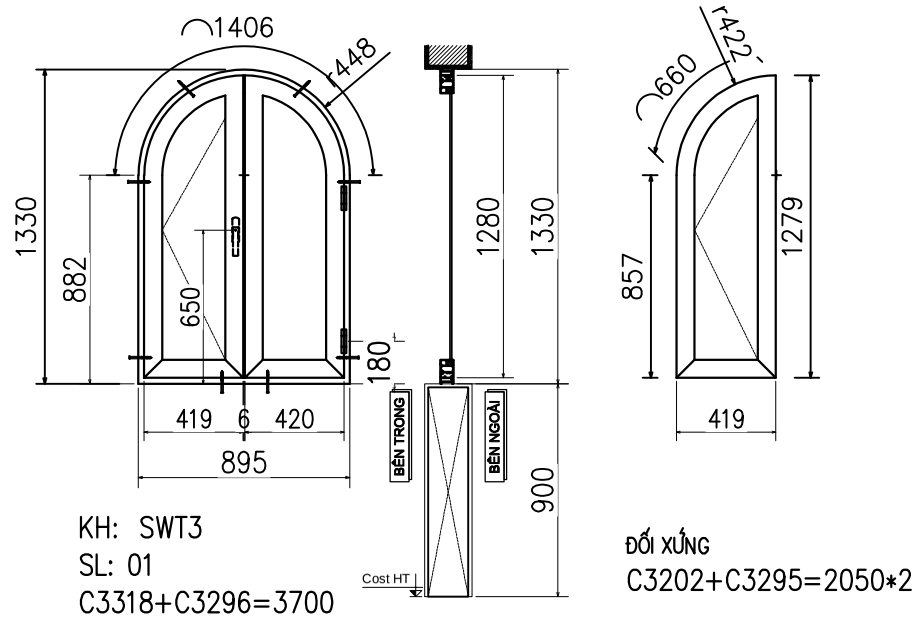


KH: SWT3
SL: 01
C3318+C3296=3700

ĐỐI XỨNG
C3202+C3295=2050*2

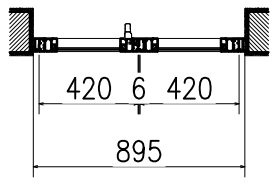

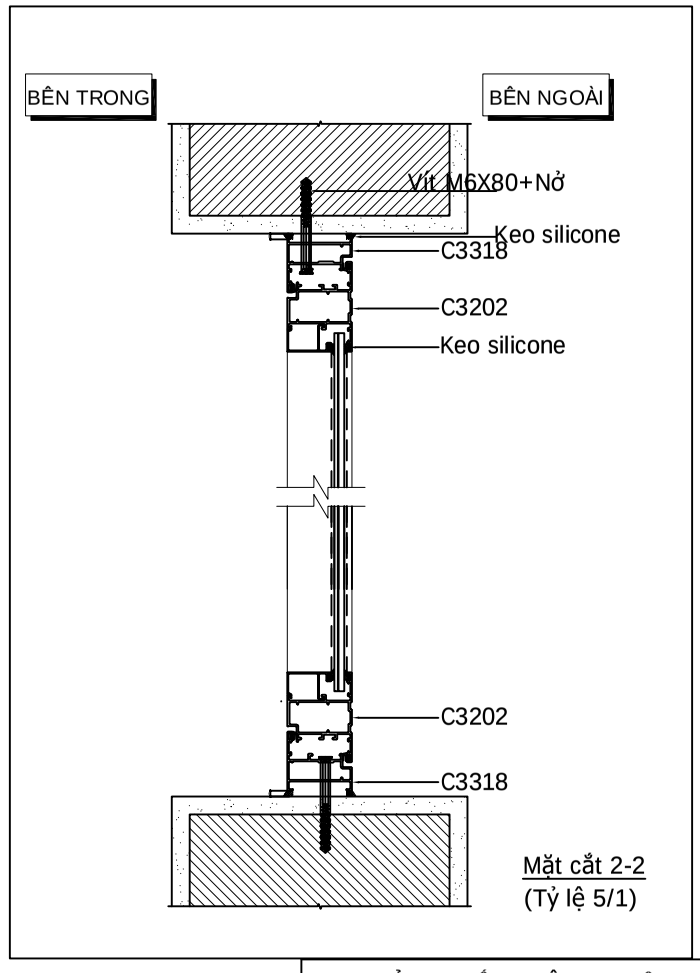

Mặt cắt 2-2
(Tỷ lệ 5/1)

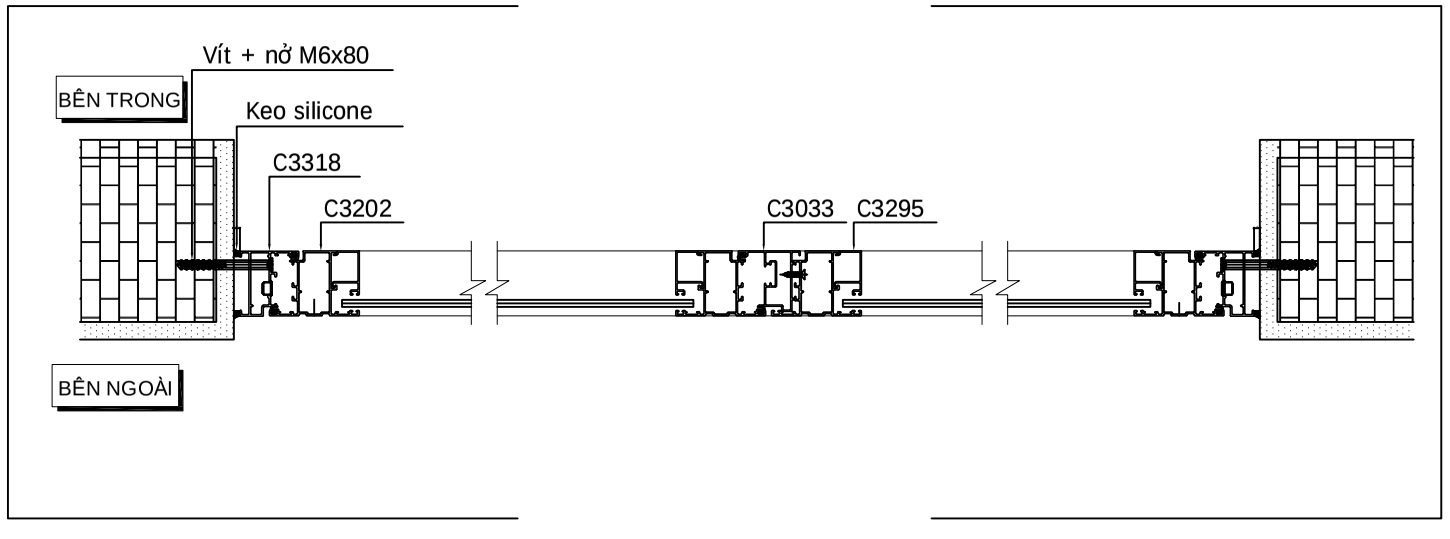

BẢNG THỐNG KÊ PHỤ KIỆN CS2 CÁNH			
Phụ kiện	Mã phụ kiện	Số lượng	Ghi chú
Bản 1D		4 cái	
Tay khoá		1 cái	Màu bạc
Thanh CĐ		1 cái	
Vấu khóa		2 cái	
Chốt âm dài		1 cái	
Chốt âm ngắn		1 cái	
Hố chốt		1 cái	
đệm chống xệ		2 bộ	
Nhựa bịt đố		1 bộ	

KH: SwT3- SL: 01 BỘ		
	QUY CÁCH	CỬA SỔ MỞ QUAY 1 CÁNH LIỀN VÁCH KÍNH
	HỆ NHÔM	XINGFA 55
	KÍNH	8.38 sữa
	SƠN	TĨNH ĐIỆN THEO MÀU PHÊ DUYỆT
VỊ TRÍ LẮP ĐẶT	PHỤ KIỆN	DAISHIN
	GHI CHÚ	HƯỚNG NHÌN TỪ BÊN NGOÀI

CHỦ ĐẦU TƯ - INVESTOR:

XÁC NHẬN CỦA TVGS & TVTK:

DỰ ÁN - PROJECT:

GÓI THẦU:
CUNG CẤP SẢN XUẤT VÀ THI CÔNG LẮP ĐẶT PHẦN CỬA ĐI, CỬA SỔ, VÁCH NHÔM KÍNH

NHÀ THẦU:
CÔNG TY CỔ NHÔM AN PHÚ
Địa chỉ: Thôn Khê Nữ - X. Phúc Thịnh - TP. Hà Nội

Chủ trì: Project manager:	
Kiểm tra: check by:	
Thiết kế: design by:	Ks. Đặng Anh Dũng

TÊN BẢN VẼ - NAME DRAWING:


Sửa đổi


Lần/rev	Ngày/date	Xác nhận/confirm

Bản vẽ số/ drawing:


Ngày tháng/date:

GHI CHÚ:
-KÍCH THƯỚC SẢN XUẤT LÀ KÍCH THƯỚC ĐỂ GIA CÔNG CỬA THÀNH PHẨM
-CHIỀU MỞ CỬA TỪNG VỊ TRÍ XEM TRÊN BẢN VẼ MẶT BẰNG
-KHOAN LỖ THOÁT NƯỚC MƯA VÀ LỖ LẮP ĐẶT TRƯỚC KHI RA CÔNG TRƯỜNG

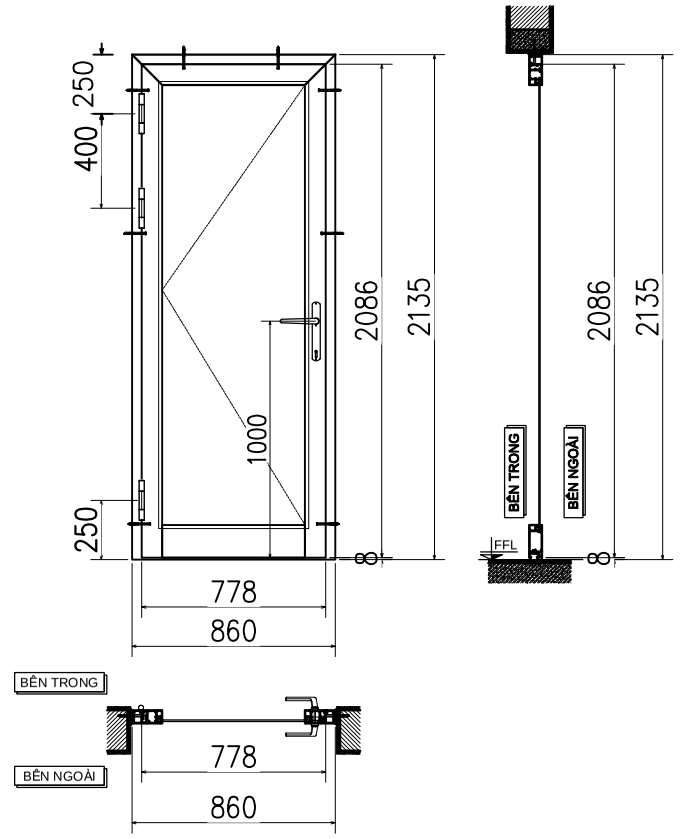

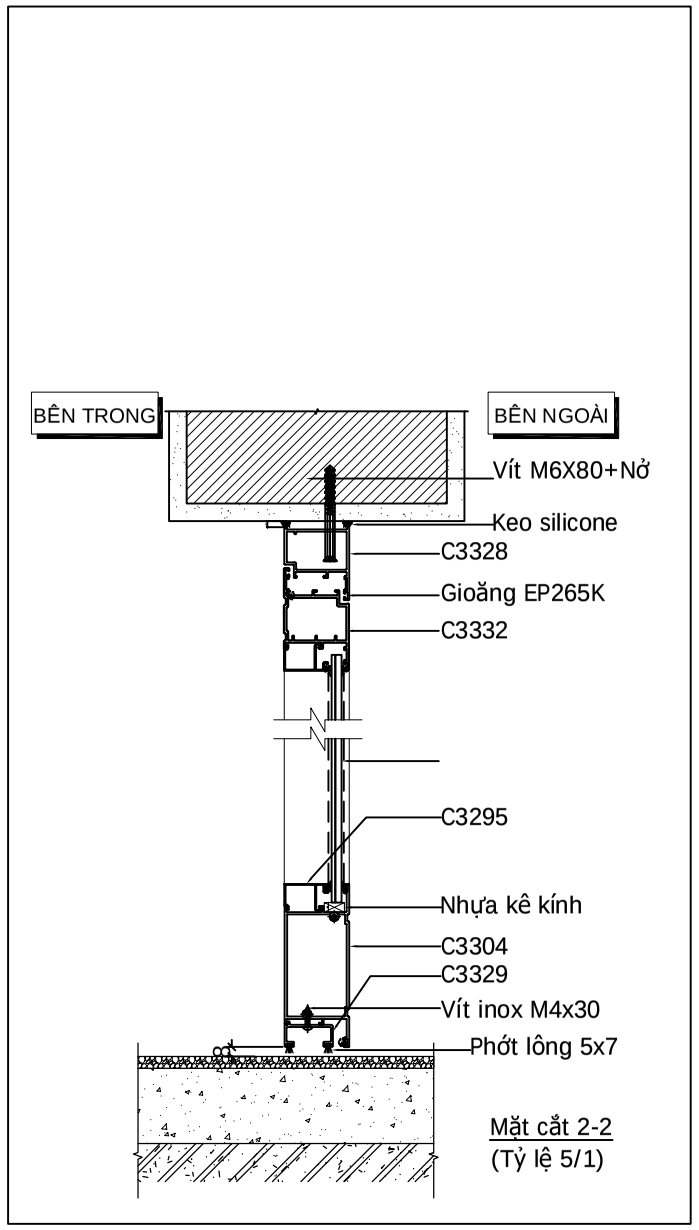

Mặt cắt 2-2
(Tỷ lệ 5/1)

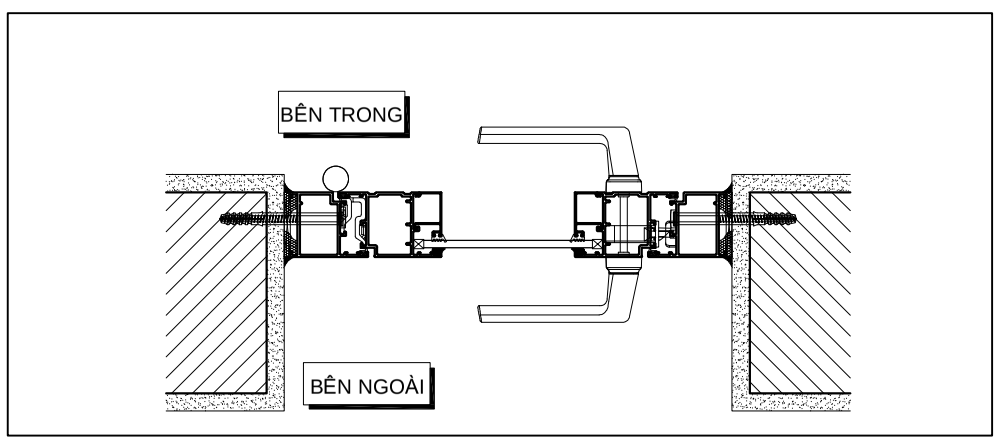

BẢNG THỐNG KÊ PHỤ KIỆN- KHÓA ĐA ĐIỂM			
Phụ kiện	Mã phụ kiện	Số lượng	Ghi chú
Bản lề bi đũa		3cái	Màu bạc
Tay khoá		1 cái	Màu bạc
Thân khoá		1 cái	Đơn ĐIỂM
Lõi khoá		1 cái	MỜ trong
		1 cái	

WCT3 SL: 01 BỘ	QUY CÁCH	CỬA SỔ MỞ QUAY 1 CÁNH LIỀN VÁCH KÍNH
	HỆ NHÔM	XINGFA 55
	KÍNH	8.38 SỮA
	SƠN	TĨNH ĐIỆN THEO MÀU PHÊ DUYỆT
VỊ TRÍ LẮP ĐẶT	PHỤ KIỆN	DAISHIN
	GHI CHÚ	HƯỚNG NHÌN TỪ BÊN NGOÀI

CHỦ ĐẦU TƯ - INVESTOR:

XÁC NHẬN CỦA TVGS & TVTK:

DỰ ÁN - PROJECT:

GÓI THẦU:
CUNG CẤP SẢN XUẤT VÀ THI CÔNG LẮP ĐẶT PHẦN CỬA ĐI, CỬA SỔ, VÁCH NHÔM KÍNH

NHÀ THẦU:
AN PHU — ANPHU WINDOW —
CÔNG TY CỔ NHÔM AN PHÚ
Địa chỉ: Thôn Khê Nữ - X. Phúc Thịnh - TP. Hà Nội


Chủ trì: Project manager:	
Kiểm tra: check by:	
Thiết kế: design by:	Ks. Đặng Anh Dũng


TÊN BẢN VẼ - NAME DRAWING:


Sửa đổi

Lần/rev	Ngày/date	Xác nhận/confirm

Bản vẽ số/ drawing:
Ngày tháng/date:

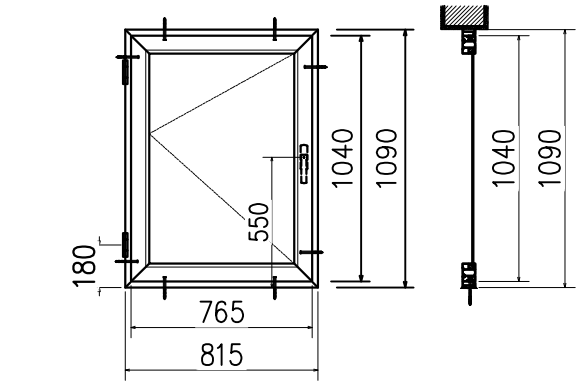


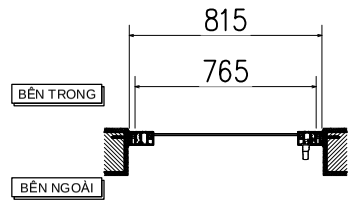

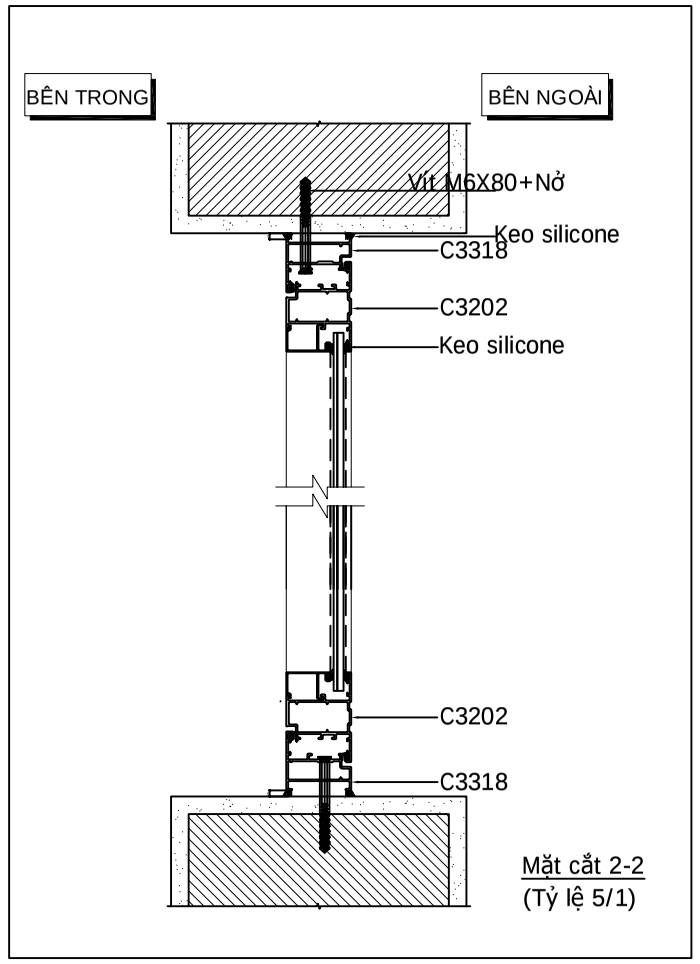

Mặt cắt 2-2
(Tỷ lệ 5/1)

CỬA KHO LÀM BẰNG HỆ CỬA SỔ, MỞ VÀO TRONG NHÀ

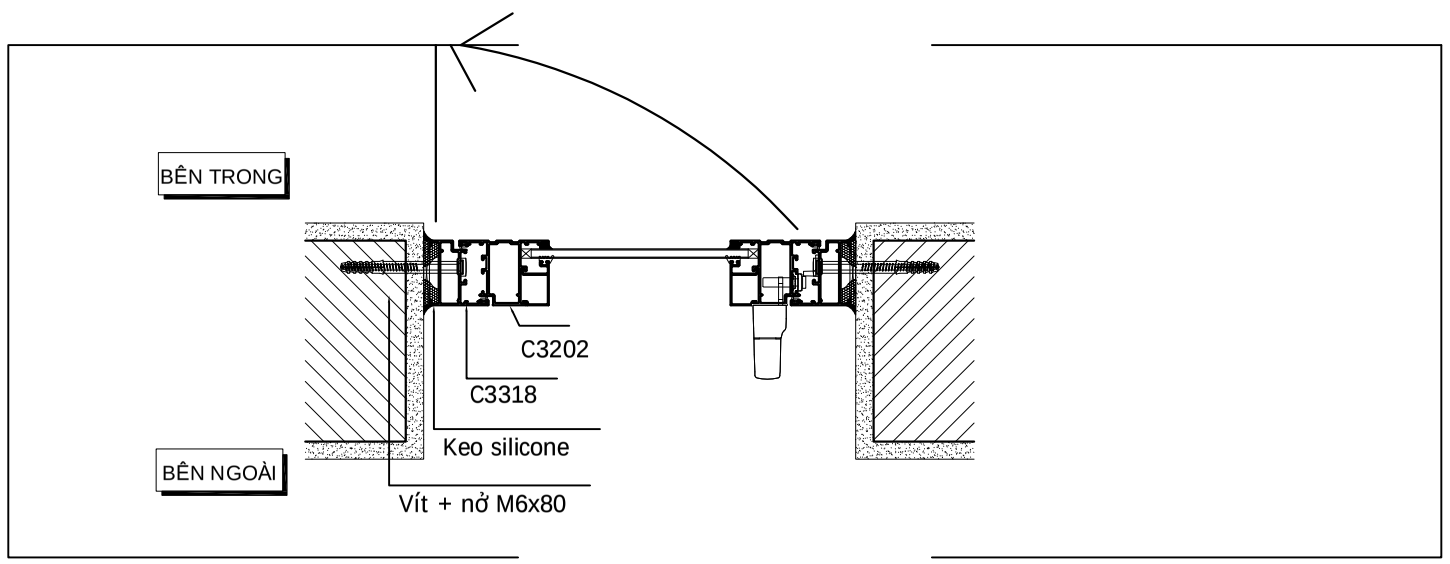

BẢNG THỐNG KÊ PHỤ KIỆN CS2 CÁNH			
Phụ kiện	Mã phụ kiện	Số lượng	Ghi chú
Bản 1D		2 cái	
Tay gài		1 cái	Màu bạc

S8T3 SL: 01	QUY CÁCH	CỬA SỔ MỞ QUAY 1 CÁNH
	HỆ NHÔM	XINGFA 55
	KÍNH	8.38 sữa
	SƠN	TĨNH ĐIỆN THEO MÀU PHÊ DUYỆT
VỊ TRÍ LẮP ĐẶT	PHỤ KIỆN	DAISHIN
	GHI CHÚ	

CHỦ ĐẦU TƯ - INVESTOR:

XÁC NHẬN CỦA TVGS & TVTK:

DỰ ÁN - PROJECT:

GÓI THẦU:

CUNG CẤP SẢN XUẤT VÀ THI CÔNG LẮP ĐẶT PHẦN CỬA ĐI, CỬA SỔ, VÁCH NHÔM KÍNH

NHÀ THẦU:

CÔNG TY CỔ NHÔM AN PHÚ

Địa chỉ: Thôn Khê Nữ - X. Phúc Thịnh - TP. Hà Nội

Chủ trì: Project manager:	
Kiểm tra: check by:	
Thiết kế: design by:	Ks. Đặng Anh Dũng

TÊN BẢN VẼ - NAME DRAWING:


Sửa đổi

Lần/rev	Ngày/date	Xác nhận/confirm

Bản vẽ số/ drawing:


Ngày tháng/date:

GHI CHÚ:
-KÍCH THƯỚC SẢN XUẤT LÀ KÍCH THƯỚC ĐỂ GIA CÔNG CỬA THÀNH PHẨM
-CHIỀU MỞ CỬA TỪNG VỊ TRÍ XEM TRÊN BẢN VẼ MẶT BẰNG
-KHOAN LỖ THOÁT NƯỚC MƯA VÀ LỖ LẮP ĐẶT TRƯỚC KHI RA CÔNG TRƯỜNG

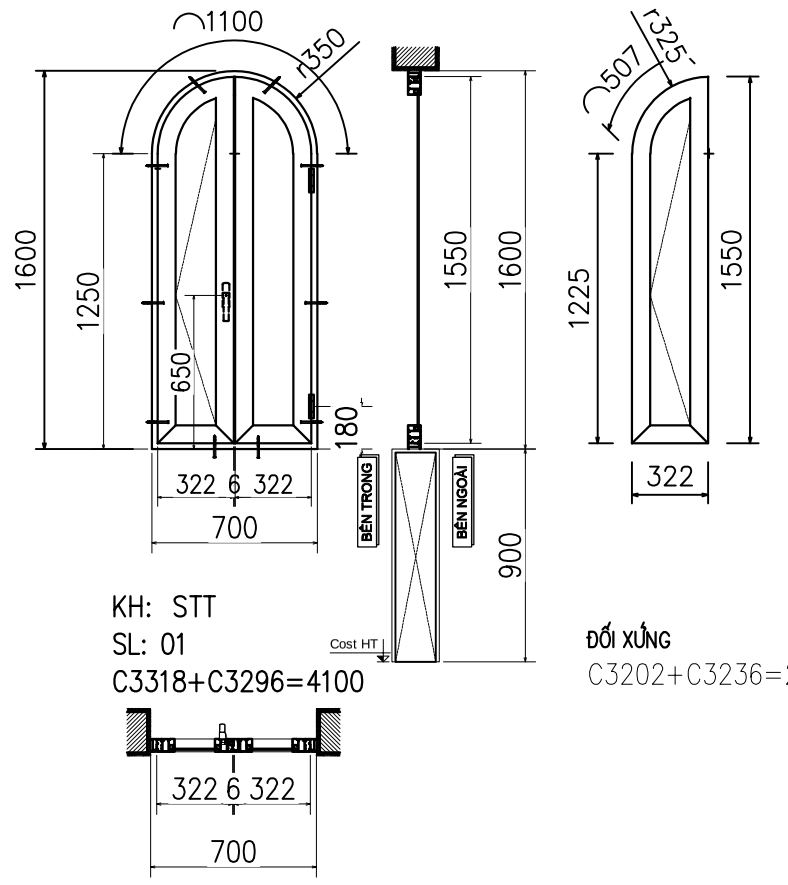


KH: STT
SL: 01
C3318+C3296=4100

ĐỐI XỨNG
C3202+C3236=2250

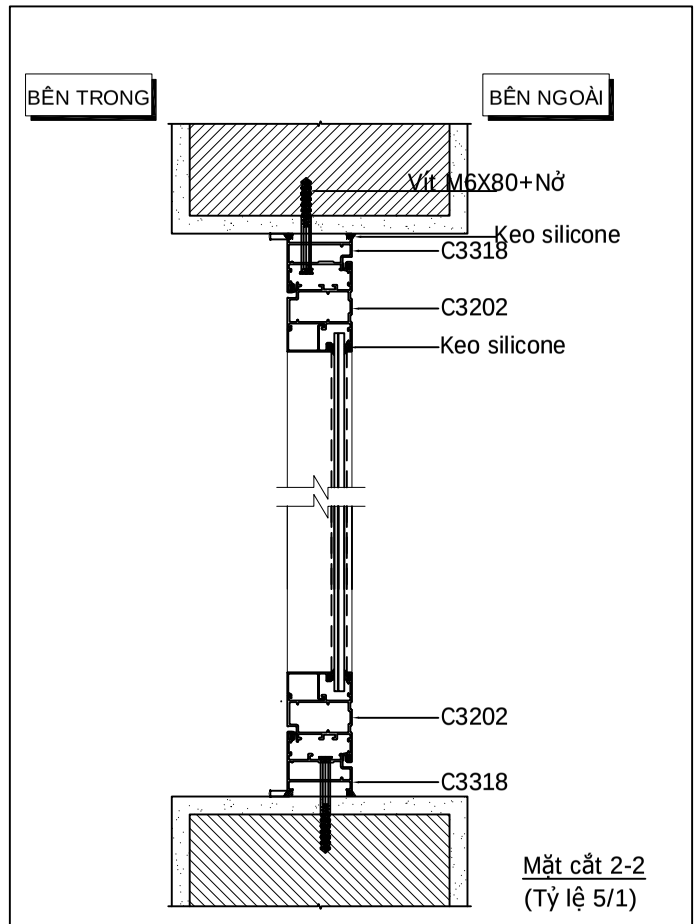

Mặt cắt 2-2
(Tỷ lệ 5/1)

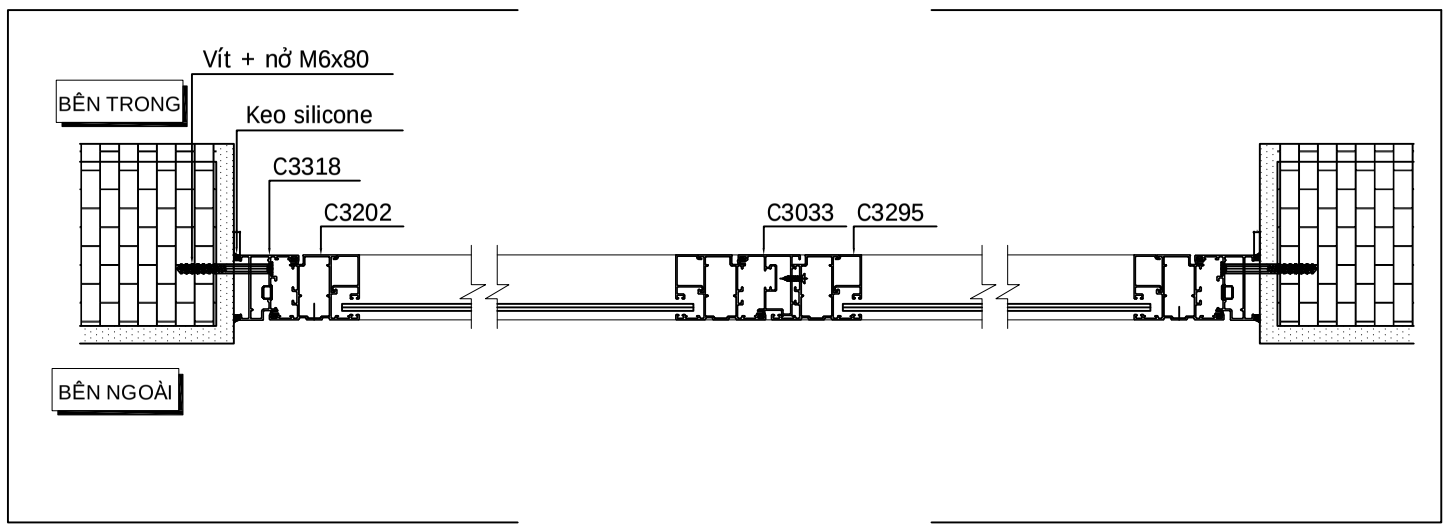

BẢNG THỐNG KÊ PHỤ KIỆN CS2 CÁNH

Phụ kiện	Mã phụ kiện	Số lượng	Ghi chú
Bản 1D		4 cái	
Tay khoá		1 cái	Màu bạc
Thanh CĐ		1 cái	
Vấu khóa		2 cái	
Chốt âm dài		1 cái	
Chốt âm ngắn		1 cái	
Hố chốt		1 cái	
đệm chống xệ		2 bộ	
Nhựa bịt đố		1 bộ	

KH:	STT	QUY CÁCH	CỬA SỔ MỞ QUAY 1 CÁNH LIỀN VÁCH KÍNH
	SL: 01 BỘ	HỆ NHÔM	XINGFA 55
		KÍNH	HỘP 19,TRONG
		SƠN	TĨNH ĐIỆN THEO MÀU PHÊ DUYỆT
VỊ TRÍ LẮP ĐẶT		PHỤ KIỆN	DAISHIN
		GHI CHÚ	HƯỚNG NHÌN TỪ BÊN NGOÀI

CHỦ ĐẦU TƯ - INVESTOR:

XÁC NHẬN CỦA TVGS & TVTK:

DỰ ÁN - PROJECT:

GÓI THẦU:
CUNG CẤP SẢN XUẤT VÀ THI CÔNG LẮP ĐẶT PHẦN CỬA ĐI, CỬA SỔ, VÁCH NHÔM KÍNH

NHÀ THẦU:
CÔNG TY CỔ NHÔM AN PHÚ
Địa chỉ: Thôn Khê Nữ - X. Phúc Thịnh - TP. Hà Nội

Chủ trì: Project manager:	
Kiểm tra: check by:	
Thiết kế: design by:	Ks. Đặng Anh Dũng

TÊN BẢN VẼ - NAME DRAWING:


Sửa đổi

Lần/rev	Ngày/date	Xác nhận/confirm


Bản vẽ số/ drawing:

Ngày tháng/date:


GHI CHÚ:
-KÍCH THƯỚC SẢN XUẤT LÀ KÍCH THƯỚC ĐỂ GIA CÔNG CỬA THÀNH PHẨM
-CHIỀU MỞ CỬA TỪNG VỊ TRÍ XEM TRÊN BẢN VẼ MẶT BẰNG
-KHOAN LỖ THOÁT NƯỚC MƯA VÀ LỖ LẮP ĐẶT TRƯỚC KHI RA CÔNG TRƯỜNG

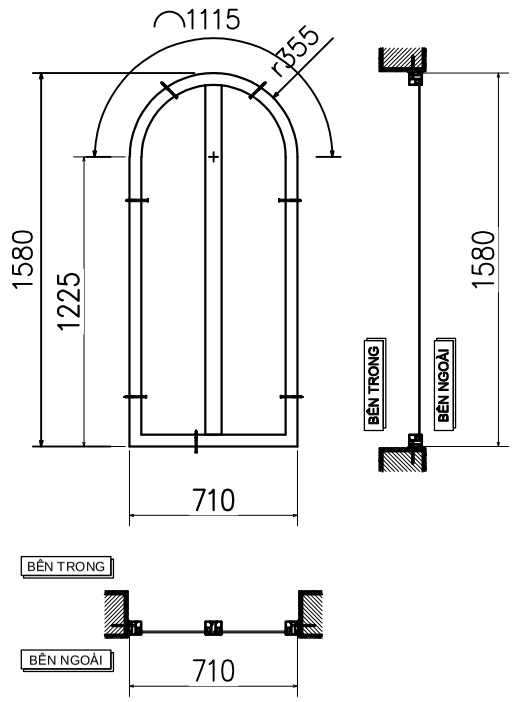


KH: V2
SL: 01
C3209+C3236=4100

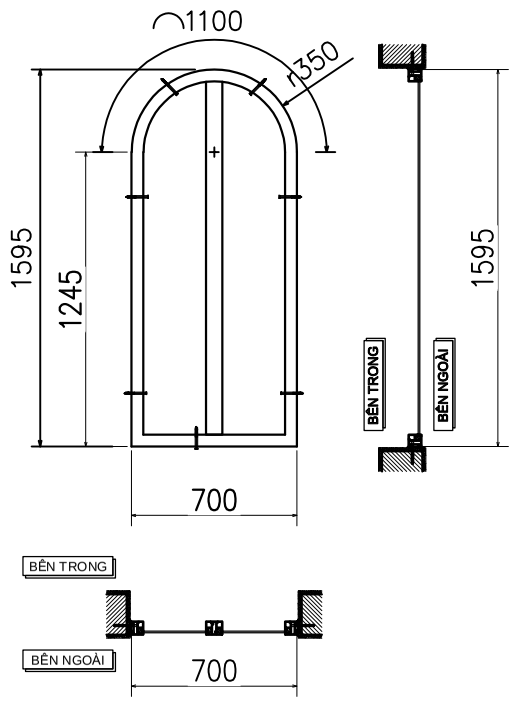


KH: V3
SL: 01
C3209+C3236=4100

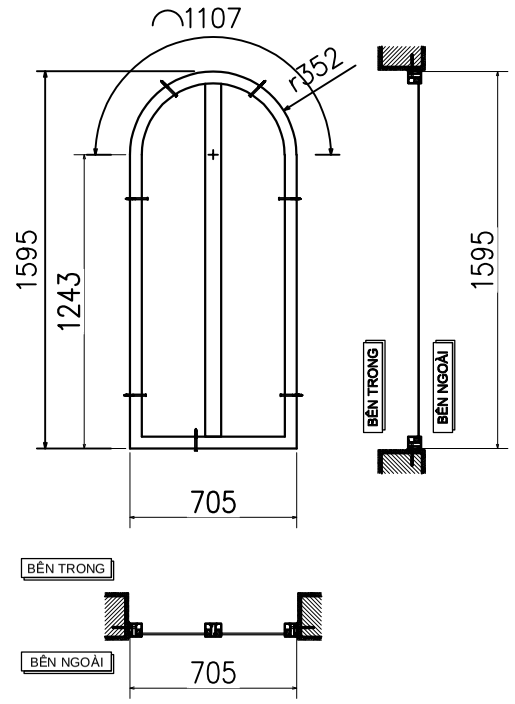


KH: V4
SL: 01
C3209+C3236=4100

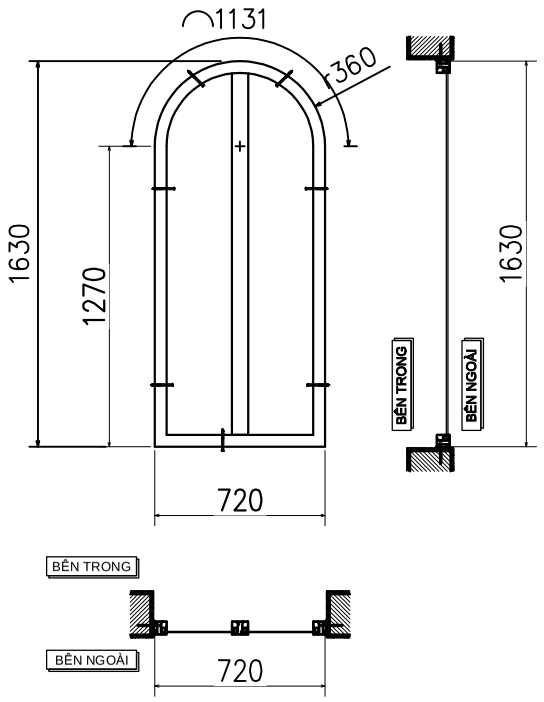

KH: V5
SL: 01
C3209+C3236=4100

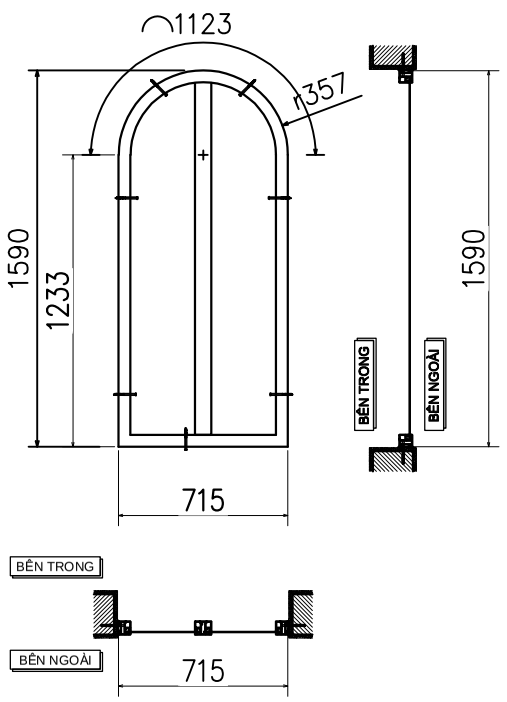

KH: V6
SL: 01
C3209+C3236=4100

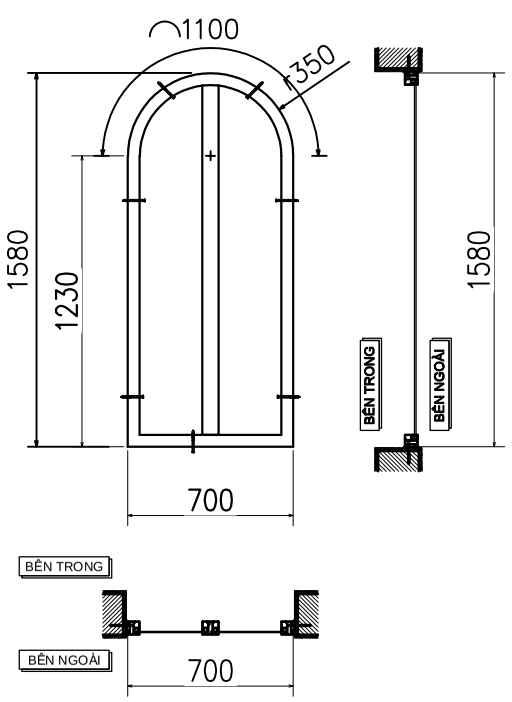

KH: V7
SL: 01
C3209+C3236=4100

CHỦ ĐẦU TƯ - INVESTOR:

XÁC NHẬN CỦA TVGS & TVTK:

DỰ ÁN - PROJECT:

GÓI THẦU:

CUNG CẤP SẢN XUẤT VÀ THI CÔNG LẮP ĐẶT PHẦN CỬA ĐI, CỬA SỔ, VÁCH NHÔM KÍNH

NHÀ THẦU:

CÔNG TY CỔ NHÔM AN PHÚ

Địa chỉ: Thôn Khê Nữ - X. Phúc Thịnh - TP. Hà Nội

Chủ trì: Project manager:	
Kiểm tra: check by:	
Thiết kế: design by:	Ks. Đặng Anh Dũng

TÊN BẢN VẼ - NAME DRAWING:

Sửa đổi

Lần/rev	Ngày/date	Xác nhận/confirm

Bản vẽ số/ drawing:

Ngày tháng/date: